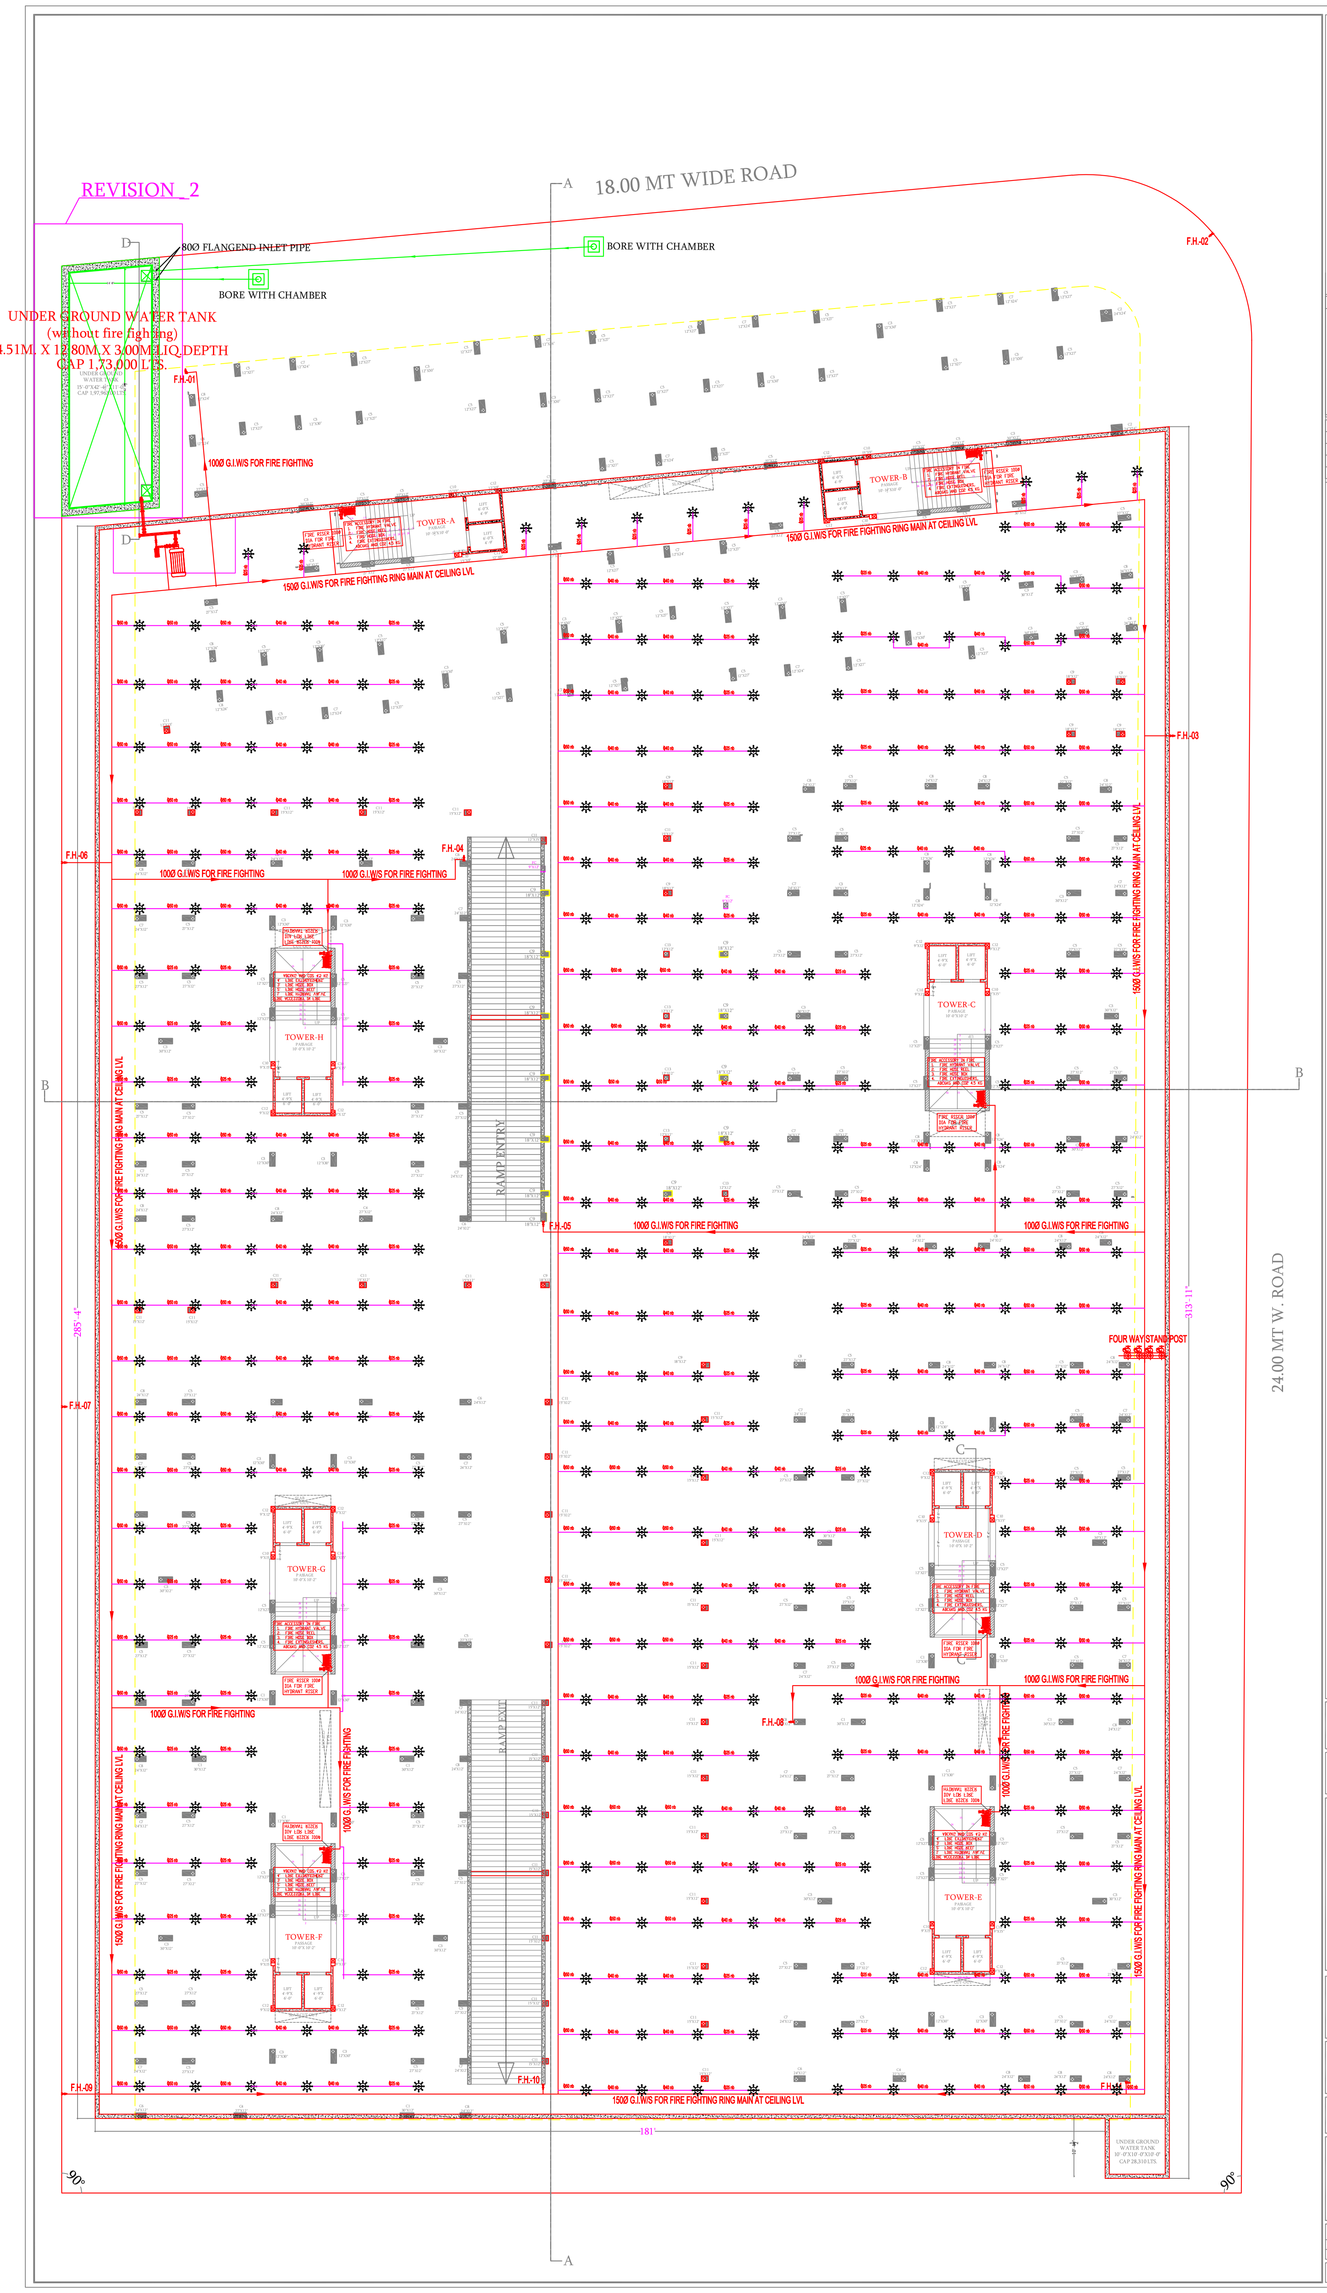

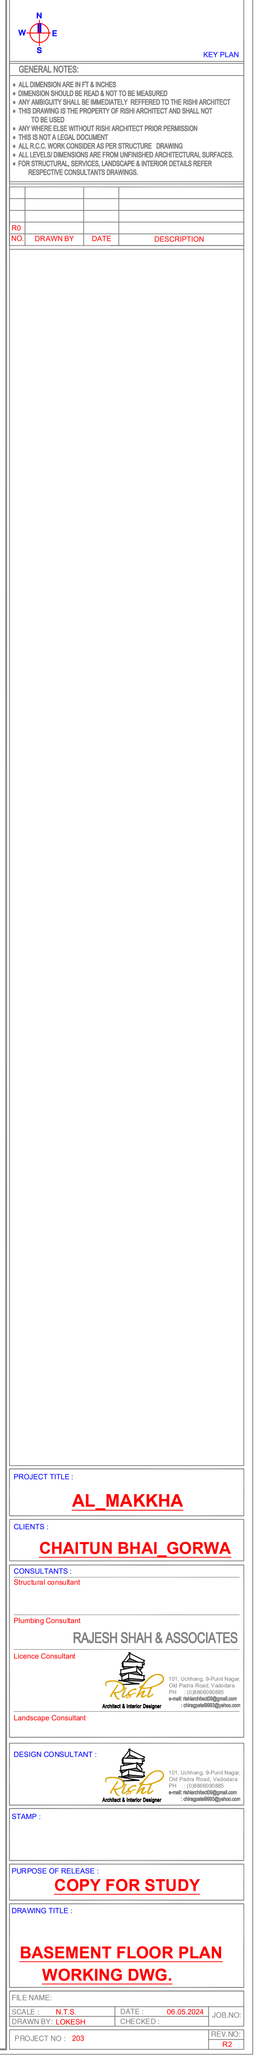

GENERAL NOTES:
- all dimensions are in ft & inches.
- dimension should be read & not to be measured.
- any ambiguity shall be immediately refer to the rishi architect.
- this drawing is the property of rishi architect and shall not to be used anywhere else with our rishi architect prior permission.
- this is not a legal document.
- all r.c.c work consider as per structure drawing.

PROJECT TITLE :
AL_MAKKHA

CLIENTS :
CHAITUN BHAI_GORWA

CONSULTANTS :
Structural consultant

Plumbing Consultant
RAJESH SHAH & ASSOCIATES

Licence Consultant
Rishi Architect & Interior Designer
101, Uchhang, 9-Punit Nagar, Old Padra Road, Vadodara
Phone : 8866090885
e-mail: rishiarchitect09@gmail.com
chiragpatel199993@yahoo.com

Landscape Consultant

DESIGN CONSULTANT :
Rishi Architect & Interior Designer
101, Uchhang, 9-Punit Nagar, Old Padra Road, Vadodara
Phone : 8866090885
e-mail: rishiarchitect09@gmail.com
chiragpatel199993@yahoo.com

STAMP :

PURPOSE OF RELEASE :
COPY FOR STUDY

DRAWING TITLE :
BASEMENT FLOOR PLAN WORKING DWG.

FILE NAME:
SCALE : N.T.S. | DATE : 06.05.2024 | JOB NO:
DRAWN BY : LOKESH | CHECKED :
PROJECT NO : 203 | REV NO : R2

BIG CAR:-74
SMALL CAR:-11
TOTAL FLAT:-224

Plot Area. :
75155.6 sq. ft.

Common Plot Area:
7515.36 sq. ft.

Drawn By.:	Checked By.:
LOKESH	TEJAS
Mail date.:	Print date.:
24.08.2023	---

Client Name:
MR. CHAITUNBHAI AT GORWA FP NO.86 TP NO.13

Drawing title:
GROUND FLOOR PLAN

Design & Licence consultants:
Rishi Architect & Interior Designer
101, Uchhang, 9 - Punit nagar, O. P. Road, Vadodara.
Phone : 8866090885
E - Mail: rishiarchitect09@gmail.com
chiragpatel199993@yahoo.com