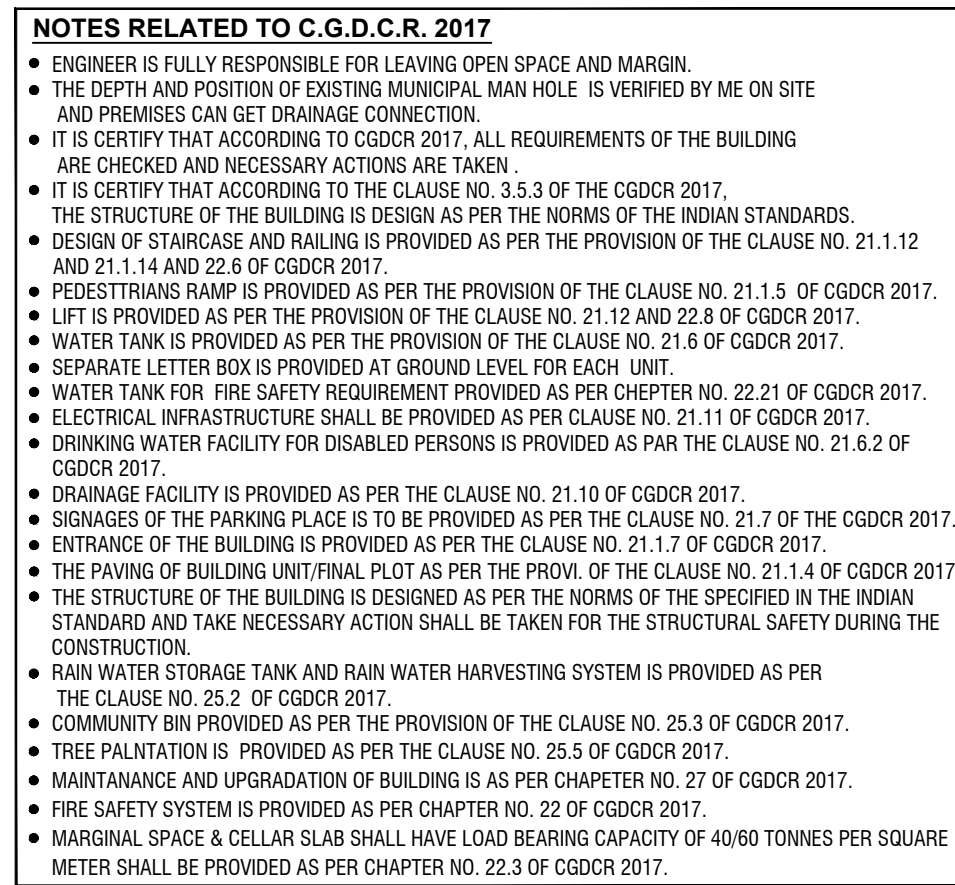


Buildingwise Floor FSI Details					
Floor Name	Building Name		Total		
	A (A)				
	Proposed Built Up Area (Sq.mt)	Proposed FSI Area (Sq.mt)	Total Proposed Built Up Area (Sq.mt)	Total FSI Area (Sq.mt)	
Ground Floor	979.41	887.61	979.41	887.61	
First Floor	705.79	566.15	705.79	566.15	
Terrace Floor	84.15	0.00	84.15	0.00	
Total:	1769.35	1453.76	1769.35	1453.76	

Building	No. of Same Bldg	Total Built Up Area (Sq.mt.)
A (A)	1	1769.35
Grand Total :	1	1769.35

Area (in Sq.mt.)					Proposed FSI Area (Sq.mt.)	Add Area in FSI (Sq.mt.)	Total FSI Area (Sq.mt.)	No. of Unit
Plot Area	Double Height Area	Ramp	Covered Area	Parking	Commercial	Parking		
166.31	60.50	12.17	0.04	211.44	1242.32	211.44	1453.76	03
166.31	60.50	12.17	0.04	211.44	1242.32	211.44	1453.76	03


Required Parking								
Building Name	Type	Sub/Use	Area	Units		Required Parking Area(Sq mt.)	Car	Other Parking
				Reqd.	Prop.			Visitor's Parking
A (A)	Mercantile	Restaurant	> 0	1	1242.32	621.16	310.58	124.23
			-					
			0 - 0	-				
	Total:					621.16	310.58	124.23

Use Type	Car				Visitor's Parking				TwoWheeler				Total Parking Area			
	Area		No.		Area		No.		Area		No.		Area		No.	
	Reqd.	Prop.	Reqd.	Prop.	Reqd.	Prop.	Reqd.	Prop.	Reqd.	Prop.	Reqd.	Prop.	Reqd.	Prop.	Reqd.	Prop.
Commercial	310.58	335.39	0	0	124.23	133.40	0	3	0.00	200.11	0	0	621.16	668.90	-	-
Total	310.58	335.39	0	0	124.23	133.40	0	3	0.00	200.11	0	0	621.16	668.90	-	-

Building/USE/SUBUSE Details											
Building Name	Building Use	Building SubUse	Building Use Group	Building Type	No Of Non-Residential Units	Floor Name	Floor Use	Floor SubUse	FSI Name	FSI Use	FSI SubUse
A (A)	Mercantile	Restaurant	Mercantile-T (MT)	3	GROUND FLOOR PLAN	Mercantile + Parking	Restaurant + Parking	Commercial FSI	Mercantile	Restaurant	
					FIRST FLOOR PLAN	Mercantile	Restaurant	Commercial FSI	Mercantile	Restaurant	
					TERRACE FLOOR PLAN	Staircase + Lift	Staircase + Lift	-	-	-	

Plot	Name	Nos Of Trees	
		Reqd	Prop
S.P.NO-02+03 OF F.P.NO-58	Tree	60	60

	<table border="1"> <thead> <tr> <th data-bbox="2739 1566 2789 1566">Name</th><th data-bbox="2789 1566 2887 1566">Prop. Area</th></tr> </thead> <tbody> <tr> <td data-bbox="2739 1566 2789 1568">COMMON PLOT</td><td data-bbox="2789 1566 2887 1568">499.62</td></tr> </tbody> </table>	Name	Prop. Area	COMMON PLOT	499.62
Name	Prop. Area				
COMMON PLOT	499.62				

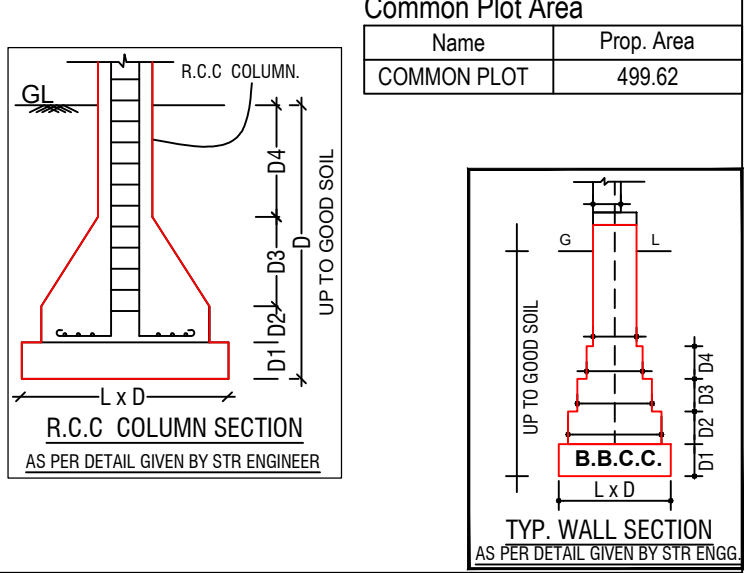




										OWNER'S NAME AND SIGNATURE BABUBAI ALBHAI MOMI	
										ARCHITECT'S NAME & SIGNATURE Rupesh Maheshkumar Dhutt	
										STRUCTURE ENGINEER MITESH GIRISHKUMAR SHAH	
										SUPERVISOR'S NAME & SIGNATURE Rupesh Maheshkumar Dhutt	
										DATE OF APPROVAL 08/10/2025	
										DESIGNATION OF APPROVER Assistant Town Development C	

UTTING	0.75	0.50	1.56	1.23	1.42	1.60	001AR04012700051	001SE14073010023
VERT LVL	29.25	29.10	29.95	29.77	29.58	29.40	SUPERVISOR'S NAME & SIGNATURE	DATE OF APPROVAL
							Rupesh Maheshkumar Bhut	08/10/2025
ROUND LVL	30.00	30.00	30.00	30.00	30.00	30.00	DESIGNATION OF APPROVER :	Assistant Town Development

ISTANCE	0.00	13.00	23.00	35.00	50.00	65.00	15110.00
---------	------	-------	-------	-------	-------	-------	-------	-------	--------	--------	---------	---------	----------	----------	

UTTING	0.75	0.50	1.56	1.23	1.42	1.60	001AR04012700051	001SE14073010023
VERT LVL	29.25	29.10	29.95	29.77	29.58	29.40	SUPERVISOR'S NAME & SIGNATURE	DATE OF APPROVAL
							Rupesh Maheshkumar Bhut	08/10/2025
ROUND LVL	30.00	30.00	30.00	30.00	30.00	30.00	DESIGNATION OF APPROVER :	Assistant Town Development

Inward No	ODPS/2025/120600	Sheet	2/3
Inward Date		Scale	1:100

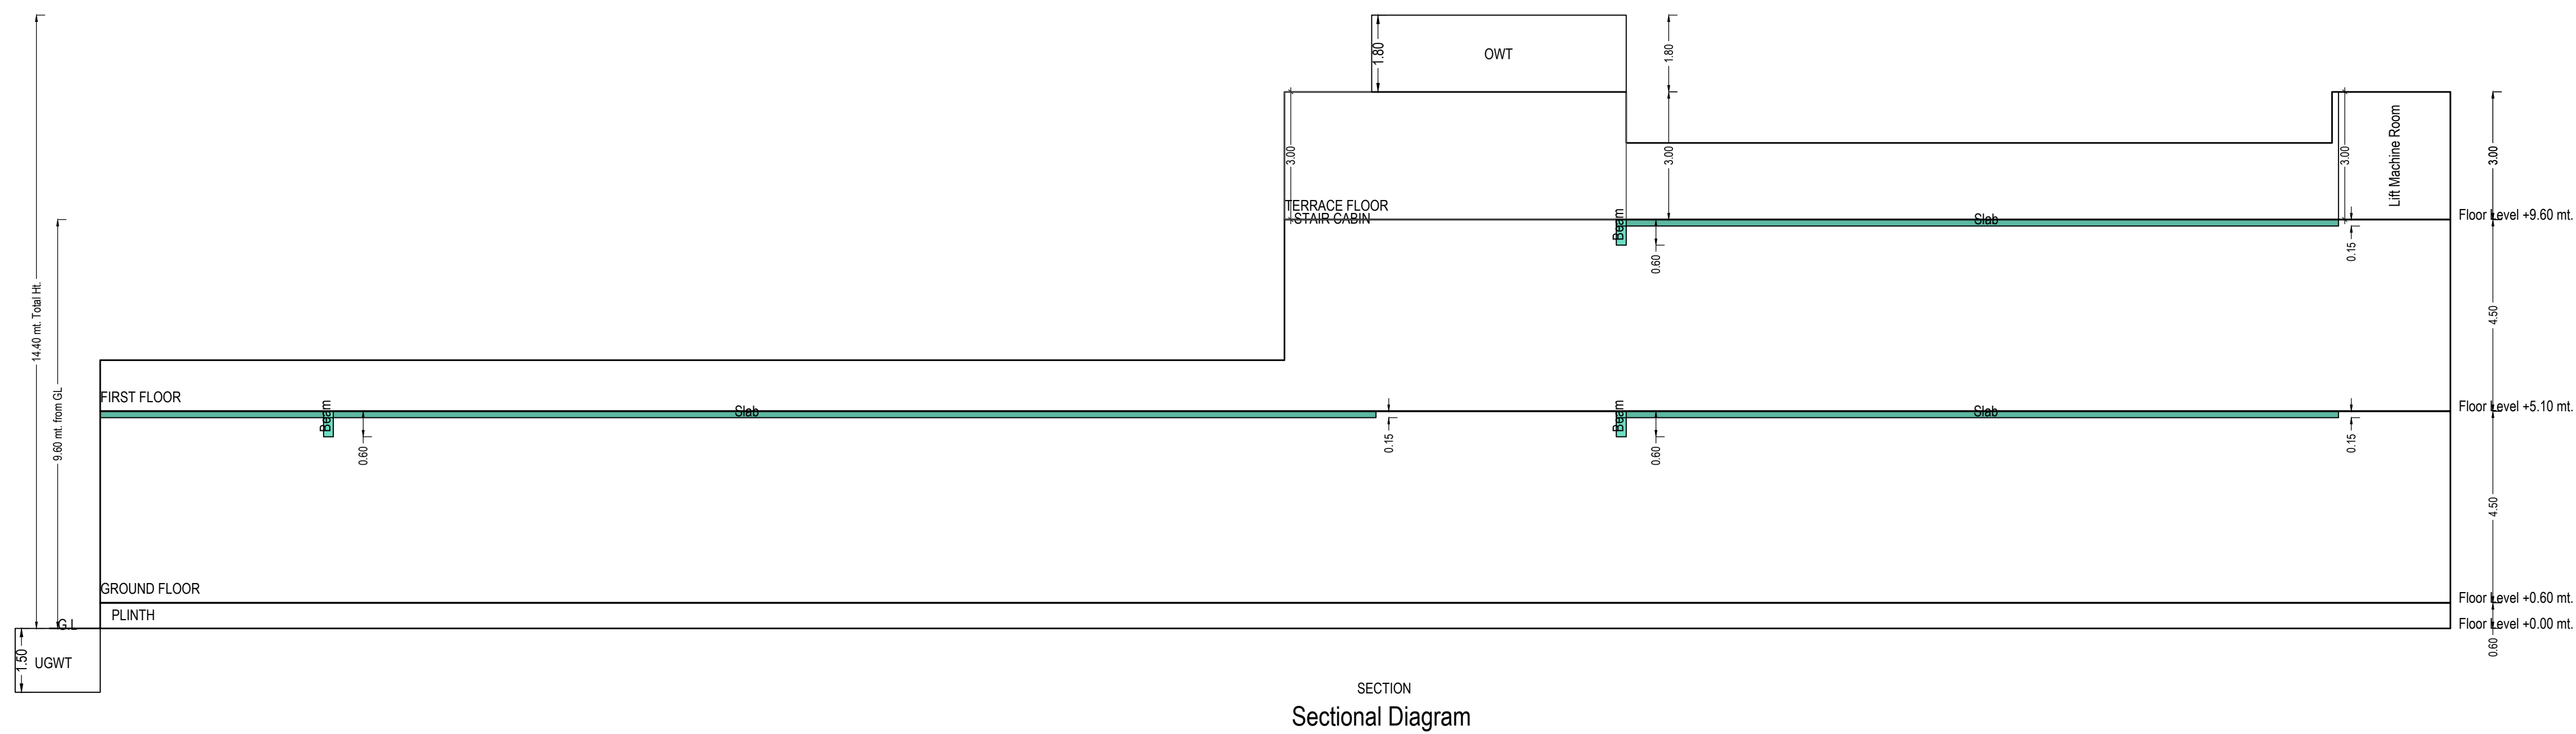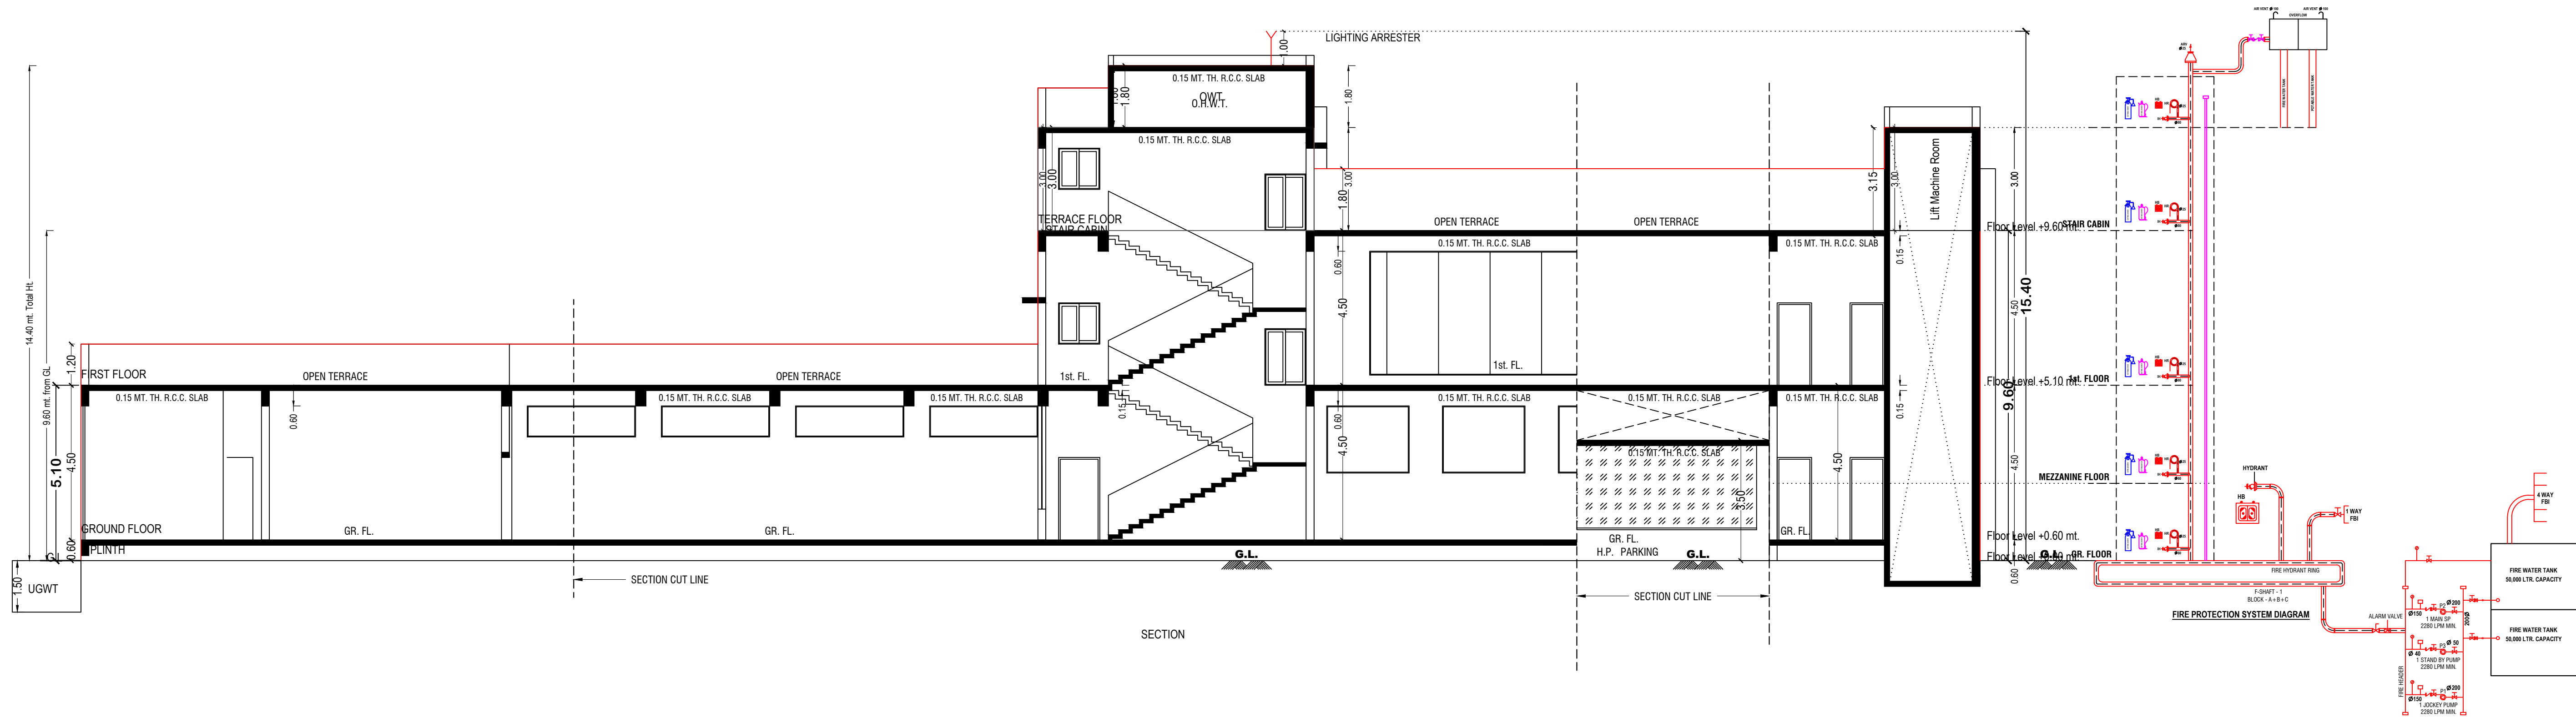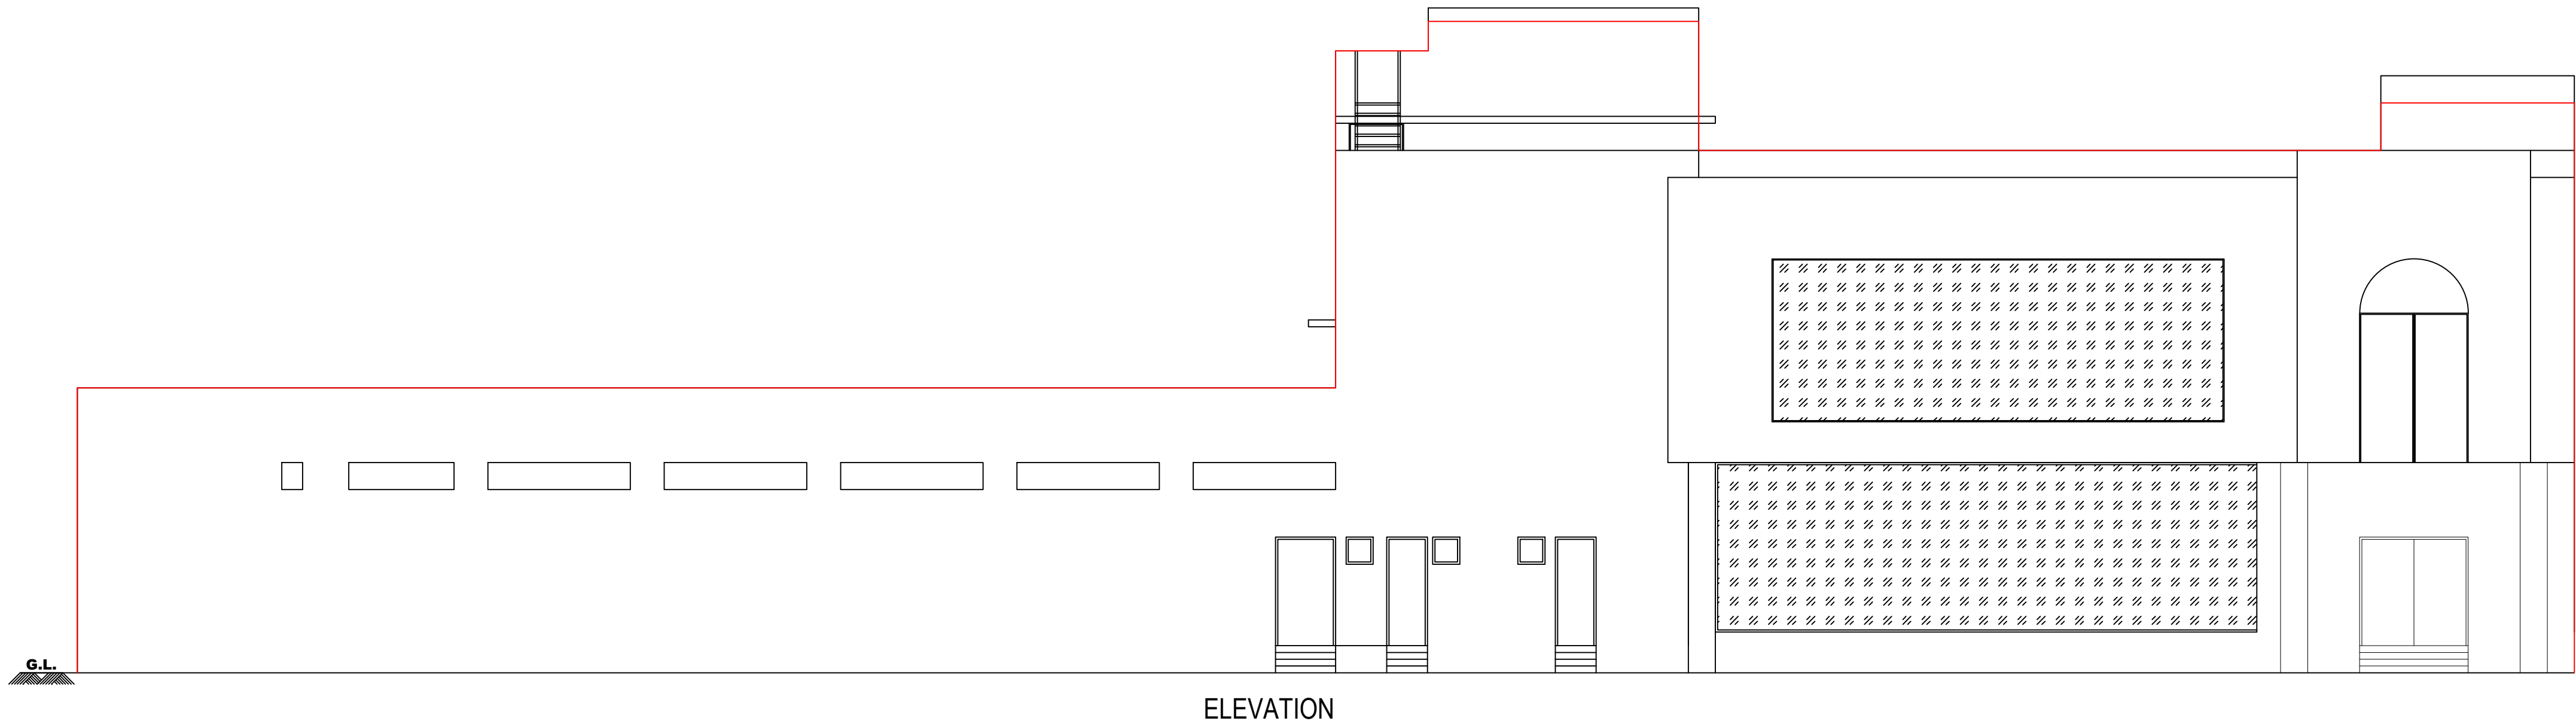

Floor Name	Total Built Up Area (Sq.mt)	Deductions from FSI/Area in Sq.mt.								Proposed FSI Area (Sq.mt.)	Add Area In FSI (Sq.mt.)	Total FSI Area (Sq.mt.)	No. of Unit
		Stair Case	Stair Lobby	Lift	Lift Machine	Lift Lobby	Double Height Area	Ramp	Covered Area				
Ground Floor	979.41	49.76	17.43	6.28	0.00	6.12	0.00	12.17	0.04	211.44		676.17	03
First Floor	705.79	48.38	18.37	6.28	0.00	6.12	60.90	0.00	0.00	566.15	0.00	566.15	00
Terrace Floor	84.15	66.40	7.40	0.00	6.28	4.07	0.00	0.00	0.00	0.00	0.00	0.00	00
Total	1769.35	164.54	43.20	12.56	6.28	16.31	60.90	12.17	0.04	211.44		1242.32	03
Total Number of Same Building	1												

UnitBUA Table for Building -A (A)									
Floor	Name	UnitBUA Type	Gross UnitBUA Area	Deductions From Gross UnitBUA Area in Sq.mt.	UnitBUA Area	Deductions (Area in Sq.mt.)	PERA Carpet Area	No. of Unit	
GROUND FLOOR PLAN	SHOP-1	OTHER	20.12	0.00	20.12	2.40	0.00	17.72	03
	SHOP-2	OTHER	20.12	0.00	20.12	2.40	0.00	17.72	
	SPLIT RESTAURANT	OTHER	715.53	12.40	703.13	46.30	67.20	636.83	
	Total per Floor	Typical Floor = 1	755.77	12.40	743.37	51.10	67.20	626.07	03
		Other	755.77	12.40	743.37	51.10	67.20	626.07	03
FIRST FLOOR PLAN	SPLIT RESTAURANT	Other	705.79	12.40	693.39	43.08	66.74	583.57	00
	Total per Floor	Typical Floor = 1	705.79	12.40	693.39	43.08	66.74	583.57	00
		Other	705.79	12.40	693.39	43.08	66.74	583.57	00
		Other	705.79	12.40	693.39	43.08	66.74	583.57	00
Total			1461.66	54.80	1406.86	94.18	1312.64	109.64	00


SCHEDULE OF DOOR:				
BUILDING NAME	NAME	LENGTH	HEIGHT	NOS
A(A)	D2	0.75	2.10	14
	D1	0.90	2.10	07
	D1	0.91	2.10	01
	D1	0.96	2.10	01
A(A)	D1	1.00	2.10	04
	G	1.10	2.10	01
	G	1.20	2.10	03
	D	1.20	2.10	03
A(A)	D	1.33	2.10	01
	D1	1.60	2.10	02
	G	1.80	2.10	01
	D	1.80	2.10	01
A(A)	D	1.85	2.10	01
	D	1.86	2.10	01
	D	2.40	2.10	01
	RS	3.40	2.10	01
A(A)	RS	3.41	2.10	01
	G	3.78	2.10	01

SCHEDULE OF WINDOW/VENTILATION:				
BUILDING NAME	NAME	LENGTH	HEIGHT	NOS
A(A)	V	0.46	1.00	02
	V	0.60	1.00	01
	V	0.60	1.00	01
	W	0.83	1.20	01
A(A)	W2	0.84	1.20	02
	W1	1.80	1.20	01
	VENT	1.82	1.00	01
	W	10.00	1.20	02
A(A)	W	12.55	1.20	01
	VENT	2.33	1.00	01
	W	2.40	1.20	16
	W1	2.40	1.20	01
A(A)	VENT	3.15	1.00	04
	W	3.15	1.20	04
	W	4.13	1.20	01
	W	6.53	1.20	01


Staircase Checks (Table 8a-1)				
Floor Name	StairCase Name	Flight Width	Tread Width	Riser Height
GROUND FLOOR PLAN	STAIRCASE	1.77	0.30	0.17
	STAIRCASE	1.50	0.30	0.17
	STAIRCASE	1.50	0.30	0.04
	STAIRCASE	1.77	0.30	0.04
FIRST FLOOR PLAN	STAIRCASE	1.50	0.30	0.00
	STAIRCASE	1.00	0.25	0.00
	STAIRCASE	1.50	0.30	0.00
	STAIRCASE	1.77	0.30	0.00

OWNER'S NAME AND SIGNATURE BABUBHAI ALIBHAI MOMIN	
ARCHENG'S NAME & SIGNATURE Rupesh Maheshkumar Bhatt	STRUCTURE ENGINEER MITESH GIRISHKUMAR SHAH
001AR04012700081	001SE14073010023
SUPERVISOR'S NAME & SIGNATURE Rupesh Maheshkumar Bhatt	
DATE OF APPROVAL 08/10/2025	
DESIGNATION OF APPROVER: Assistant Town Development Officer	




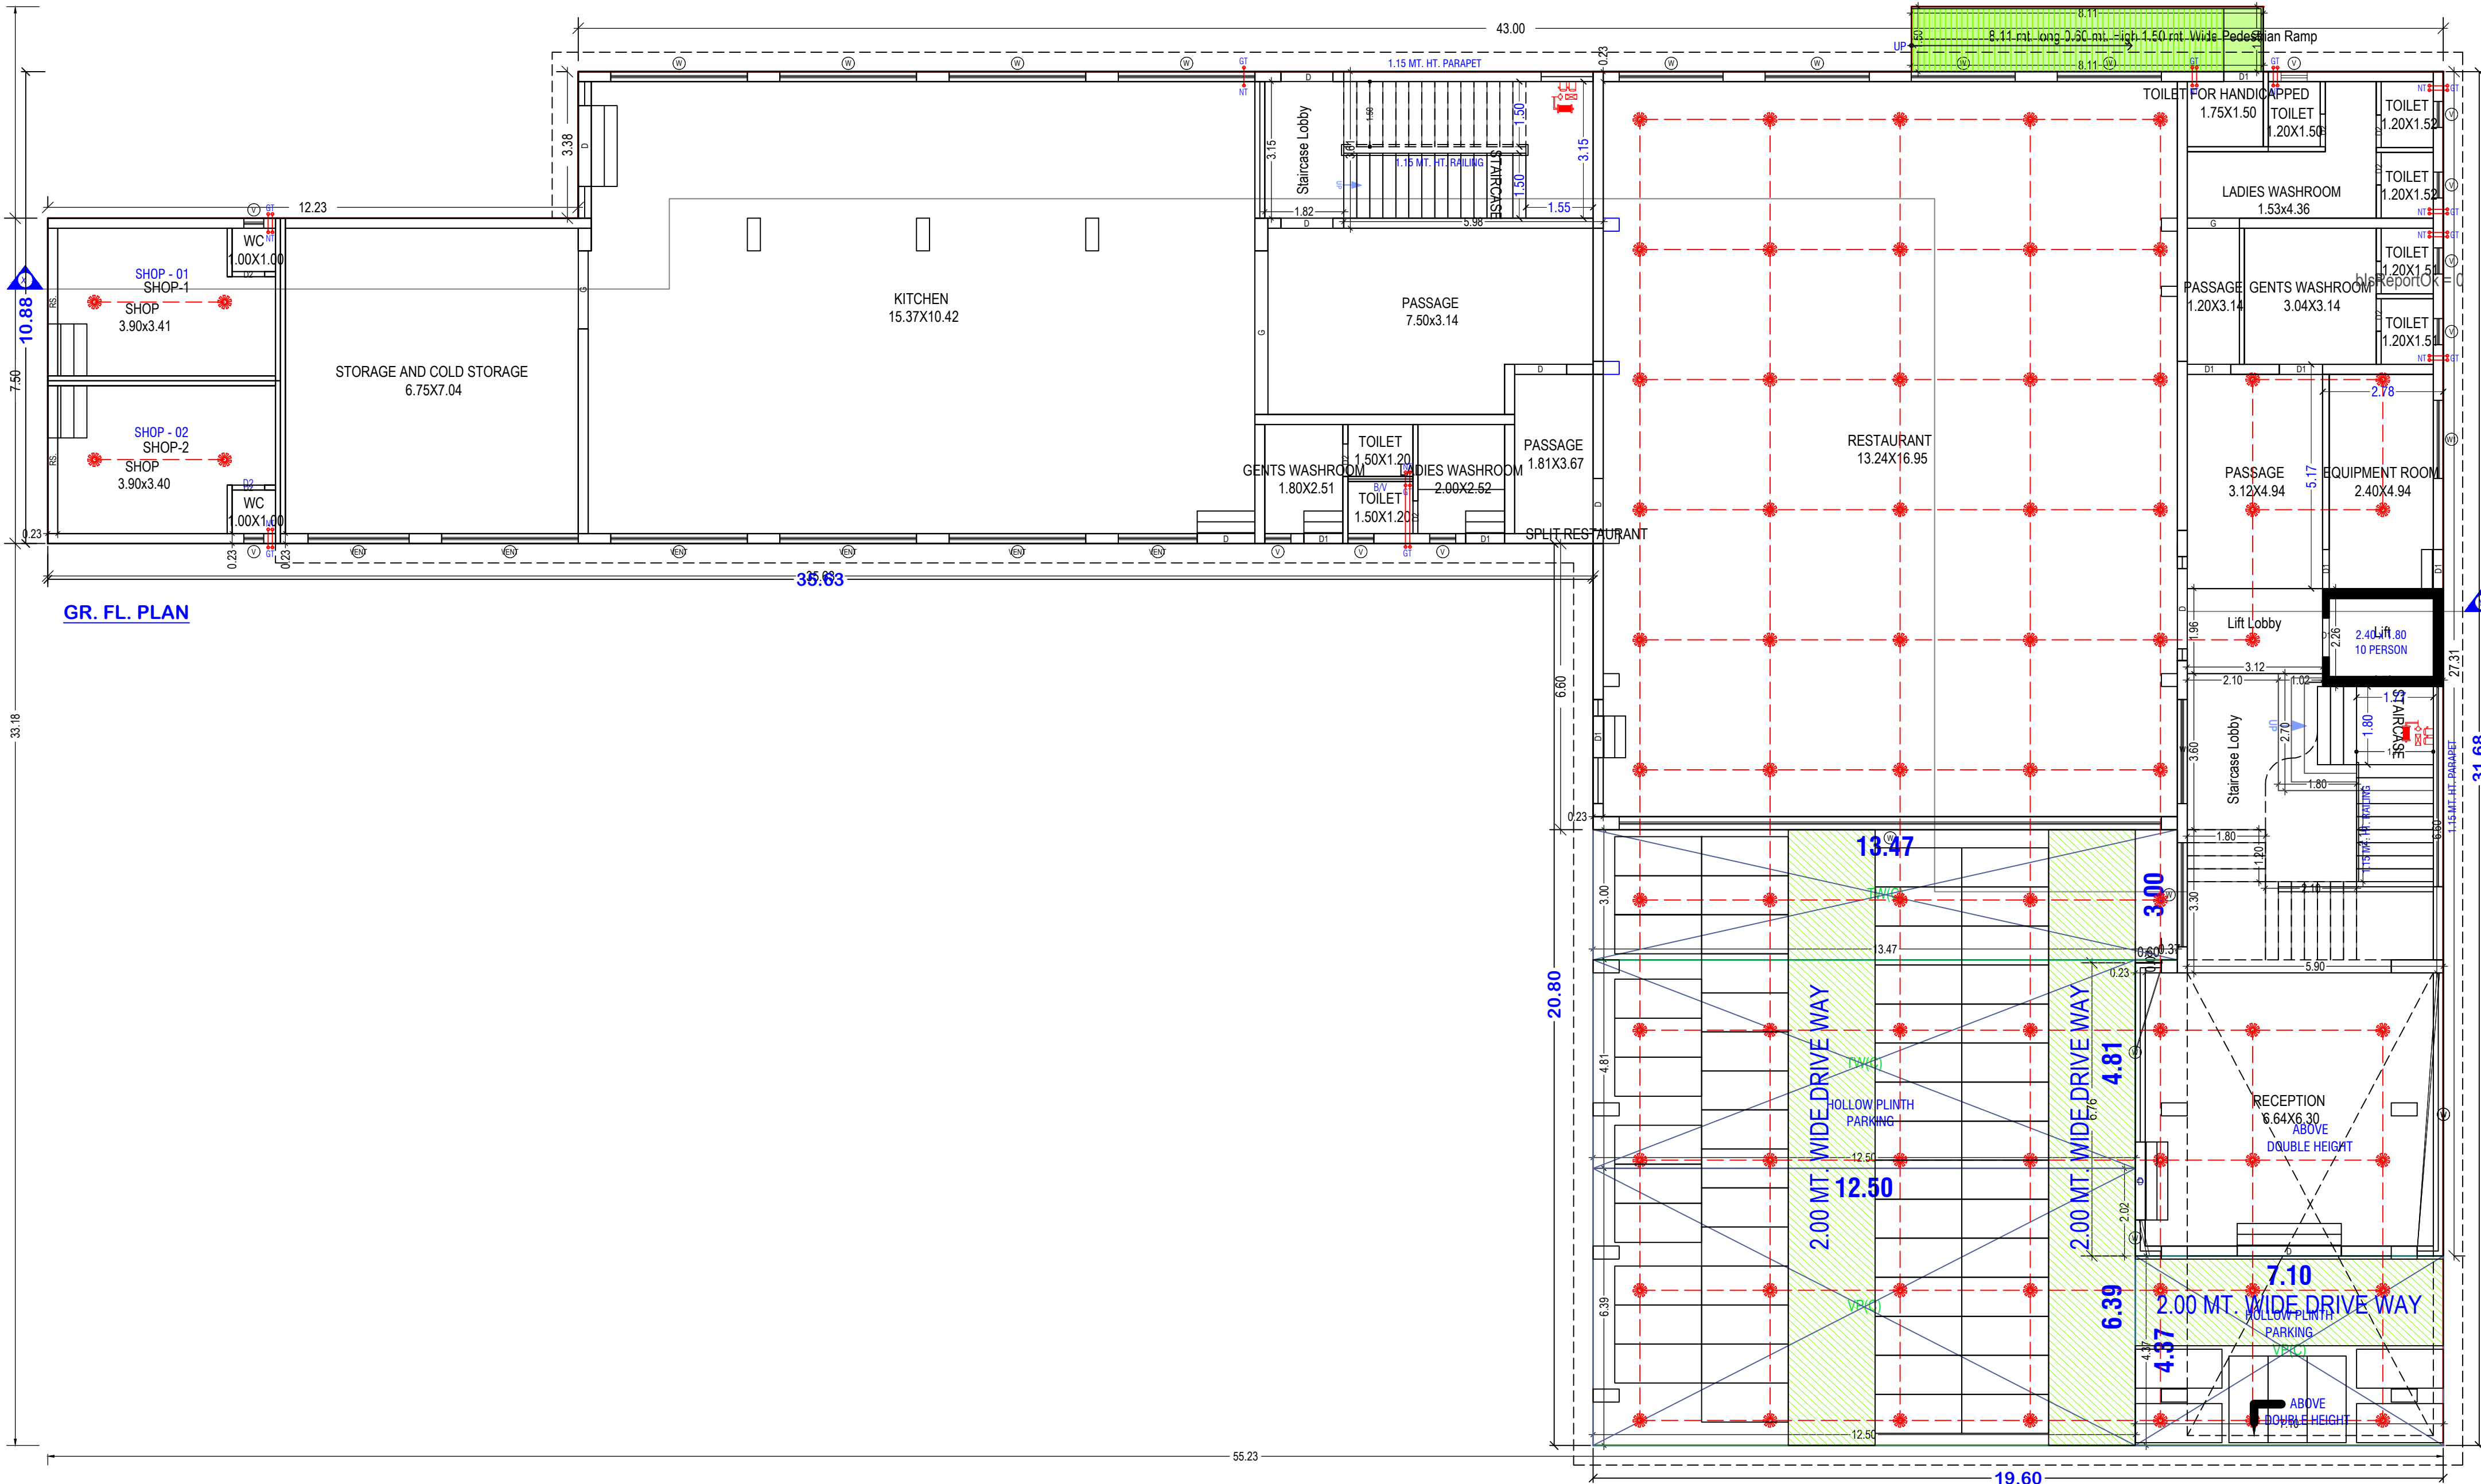

GROUND FLOOR PLAN
(Proposed)
(SCALE 1:100)

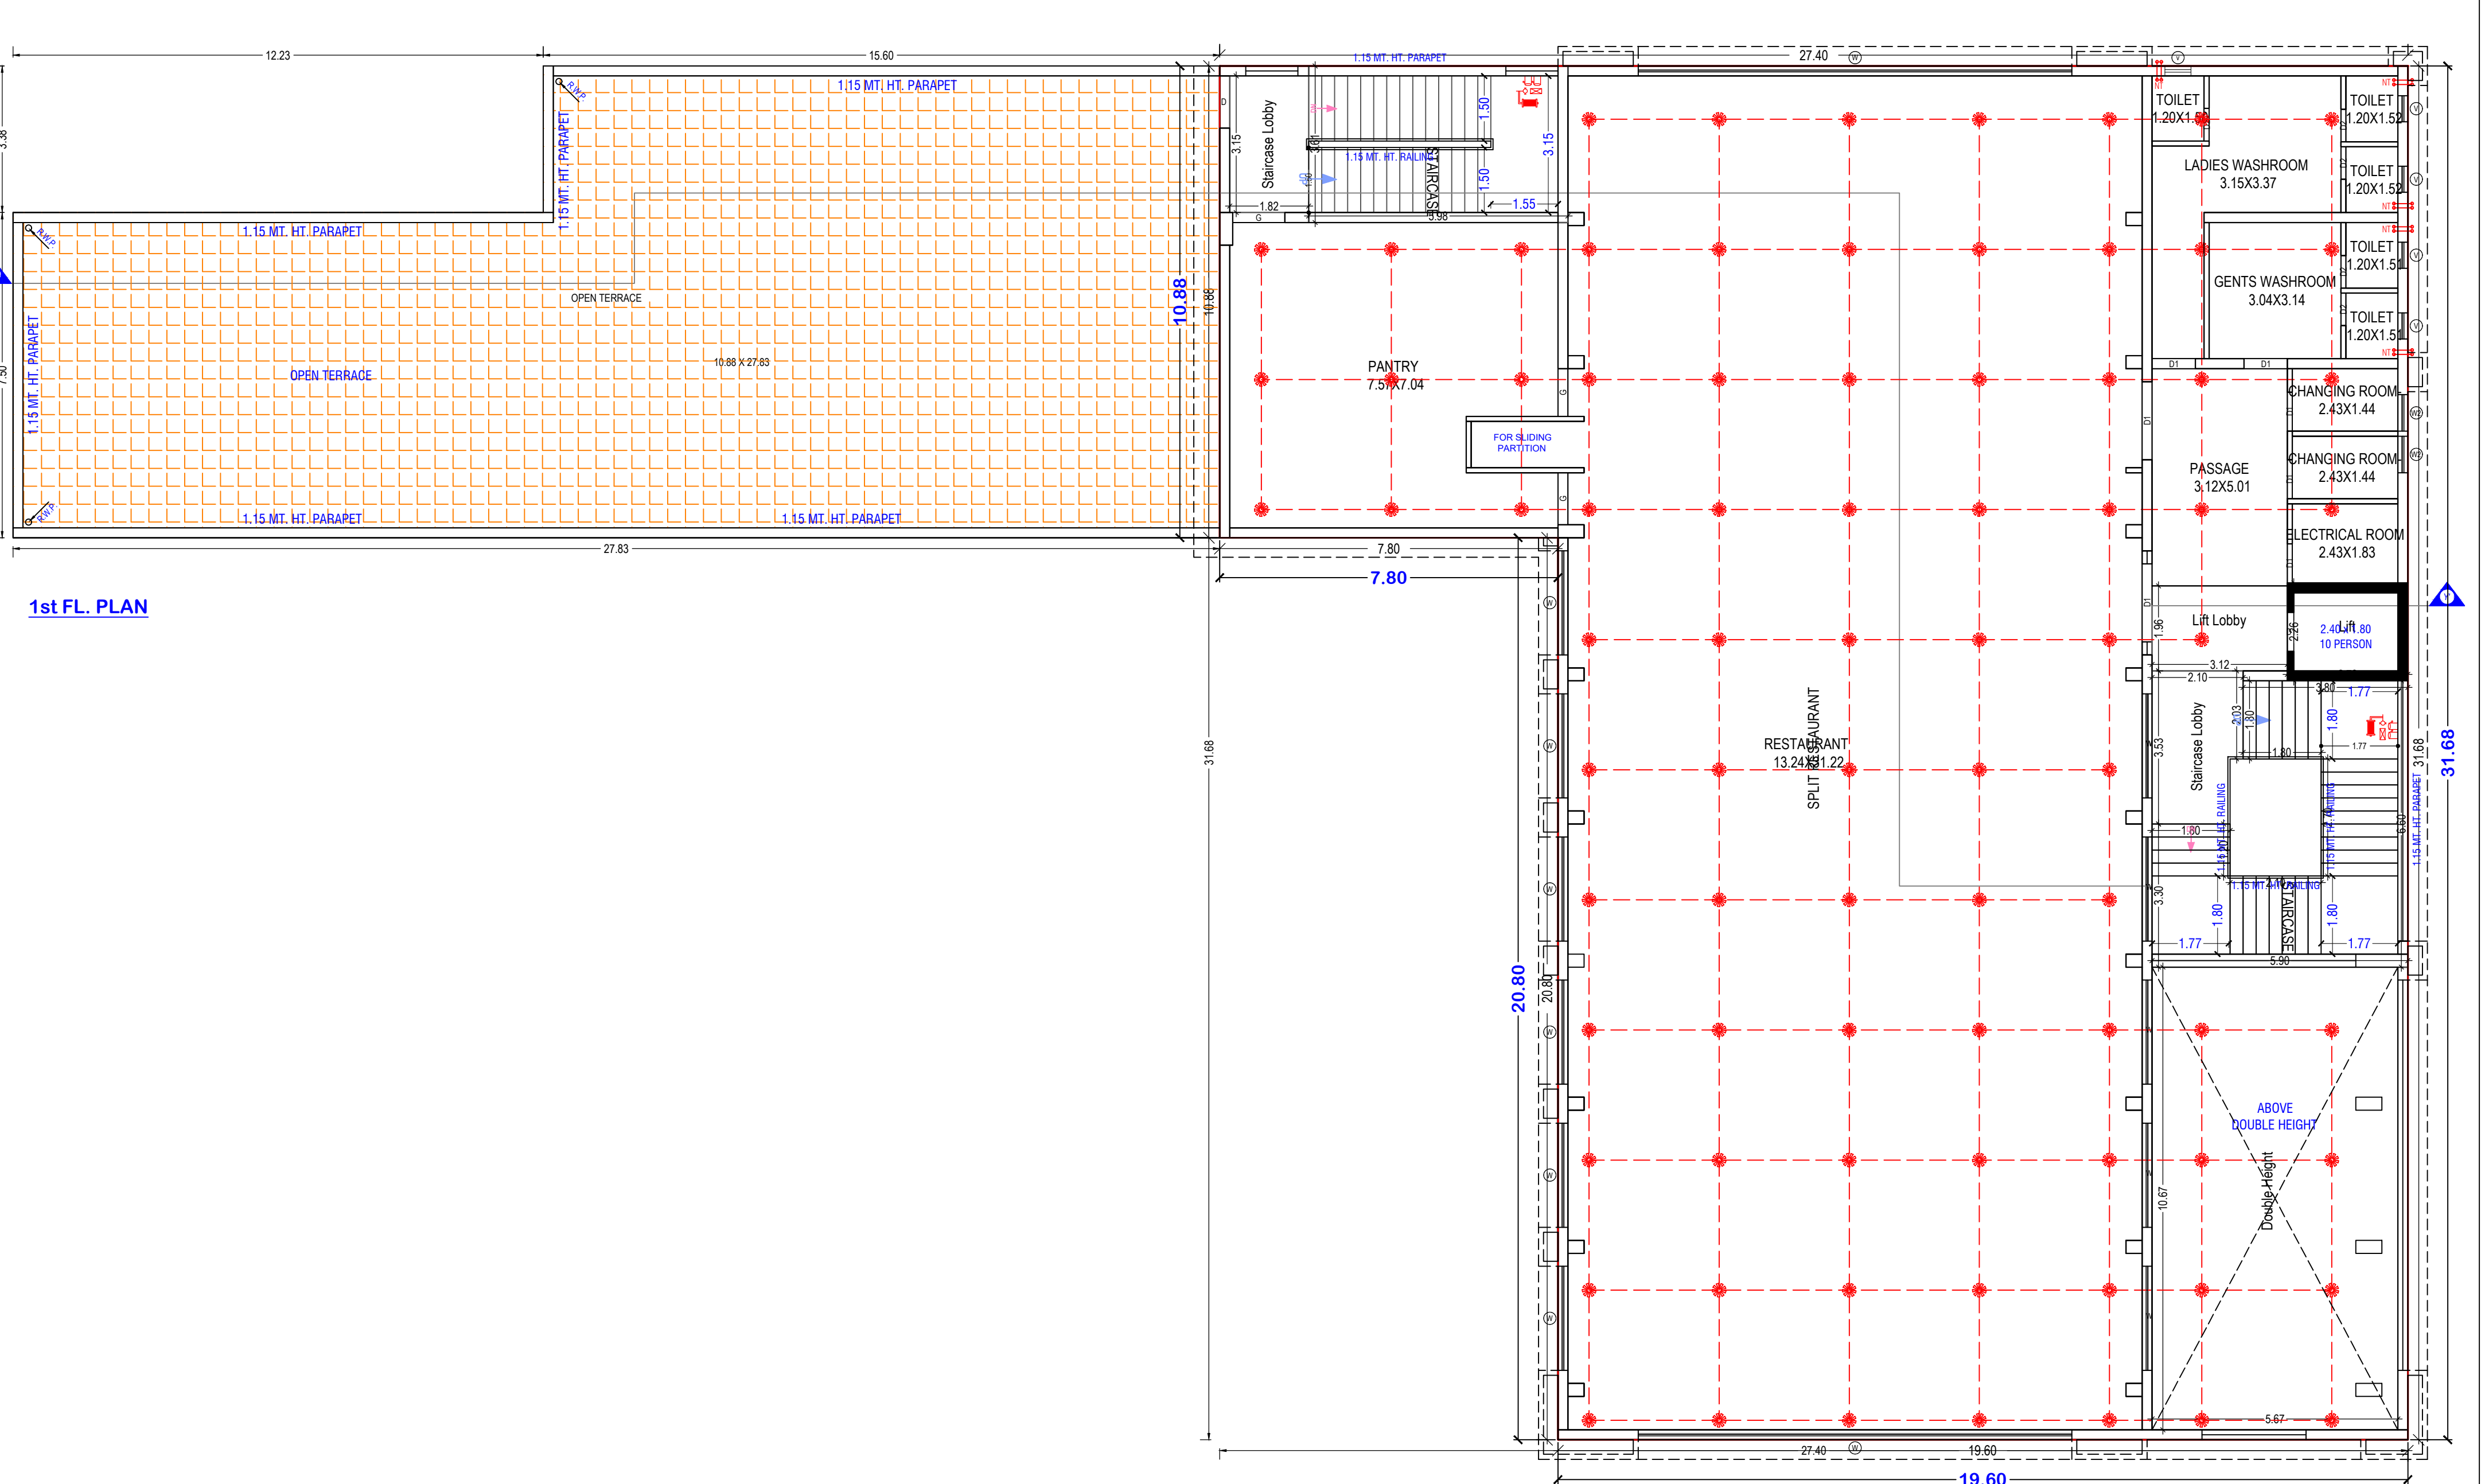

FIRST FLOOR PLAN
(Proposed)
(SCALE 1:100)

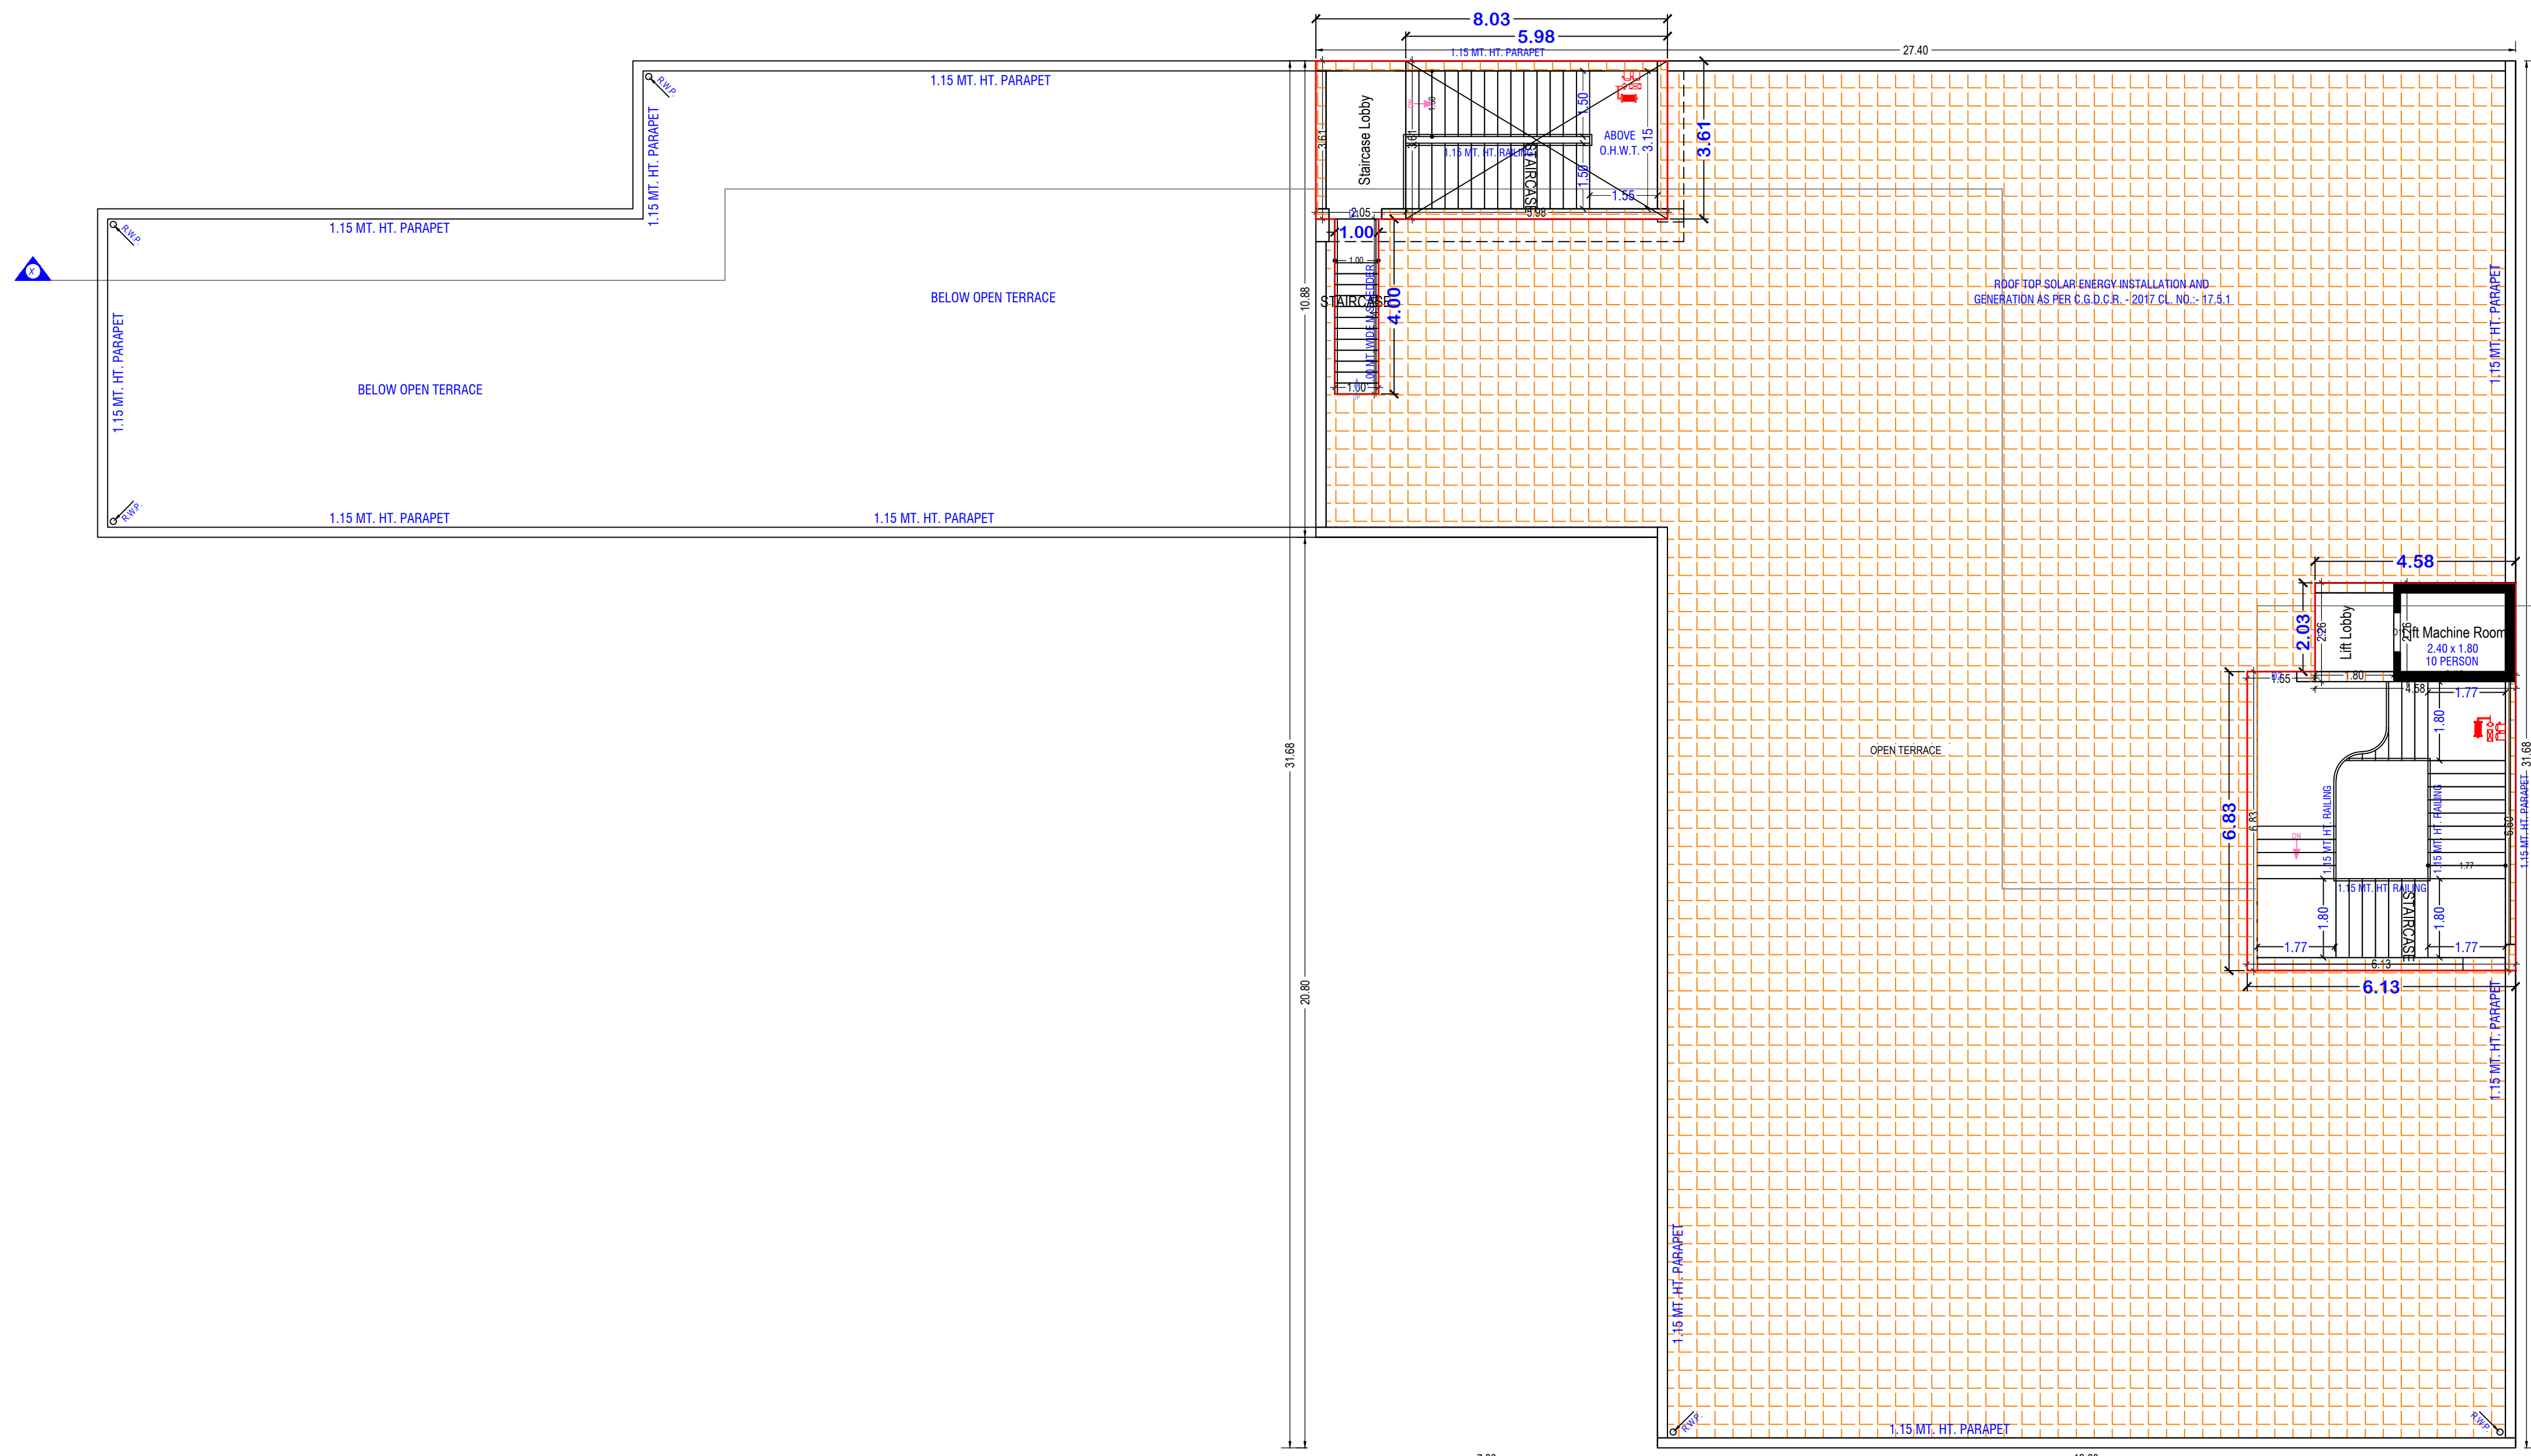

TERRACE FLOOR PLAN
(SCALE 1:100)