


NOTES:

1. DO NOT SCALE THE DRAWING.
2. ALL DIMENSIONS ARE IN METER.
3. ALL MEASUREMENTS ARE TO BE CHECKED AND VERIFIED ON THE SITE.
4. ANY DISCREPANCIES IN DRAWINGS MUST BE CLARIFIED WITH THE CONSULTANT PRIOR TO EXECUTION.

LEGEND:-

	TERRACE BOOSTER PUMP 900 LPM
	100Ø FIRE DOWNCOMER
	BALL VALVE
	FIRST AID HOSE REEL WITH DRUM
	2WAY FIRE BRIGADE
	FA CABLE-2C X 1.5 SM
	HOOTER / MANUAL CALL POINT
	FIRE ALARM CONTROL PANEL
	BFV- BUTTERFLY VALVE
	G.I. PIPE
	FIRE PUMP PANEL
	Co2 TYPE FIRE EXTINGUISHER (4.5 KG.)
	ABC TYPE FIRE EXTINGUISHER (6 KG.)

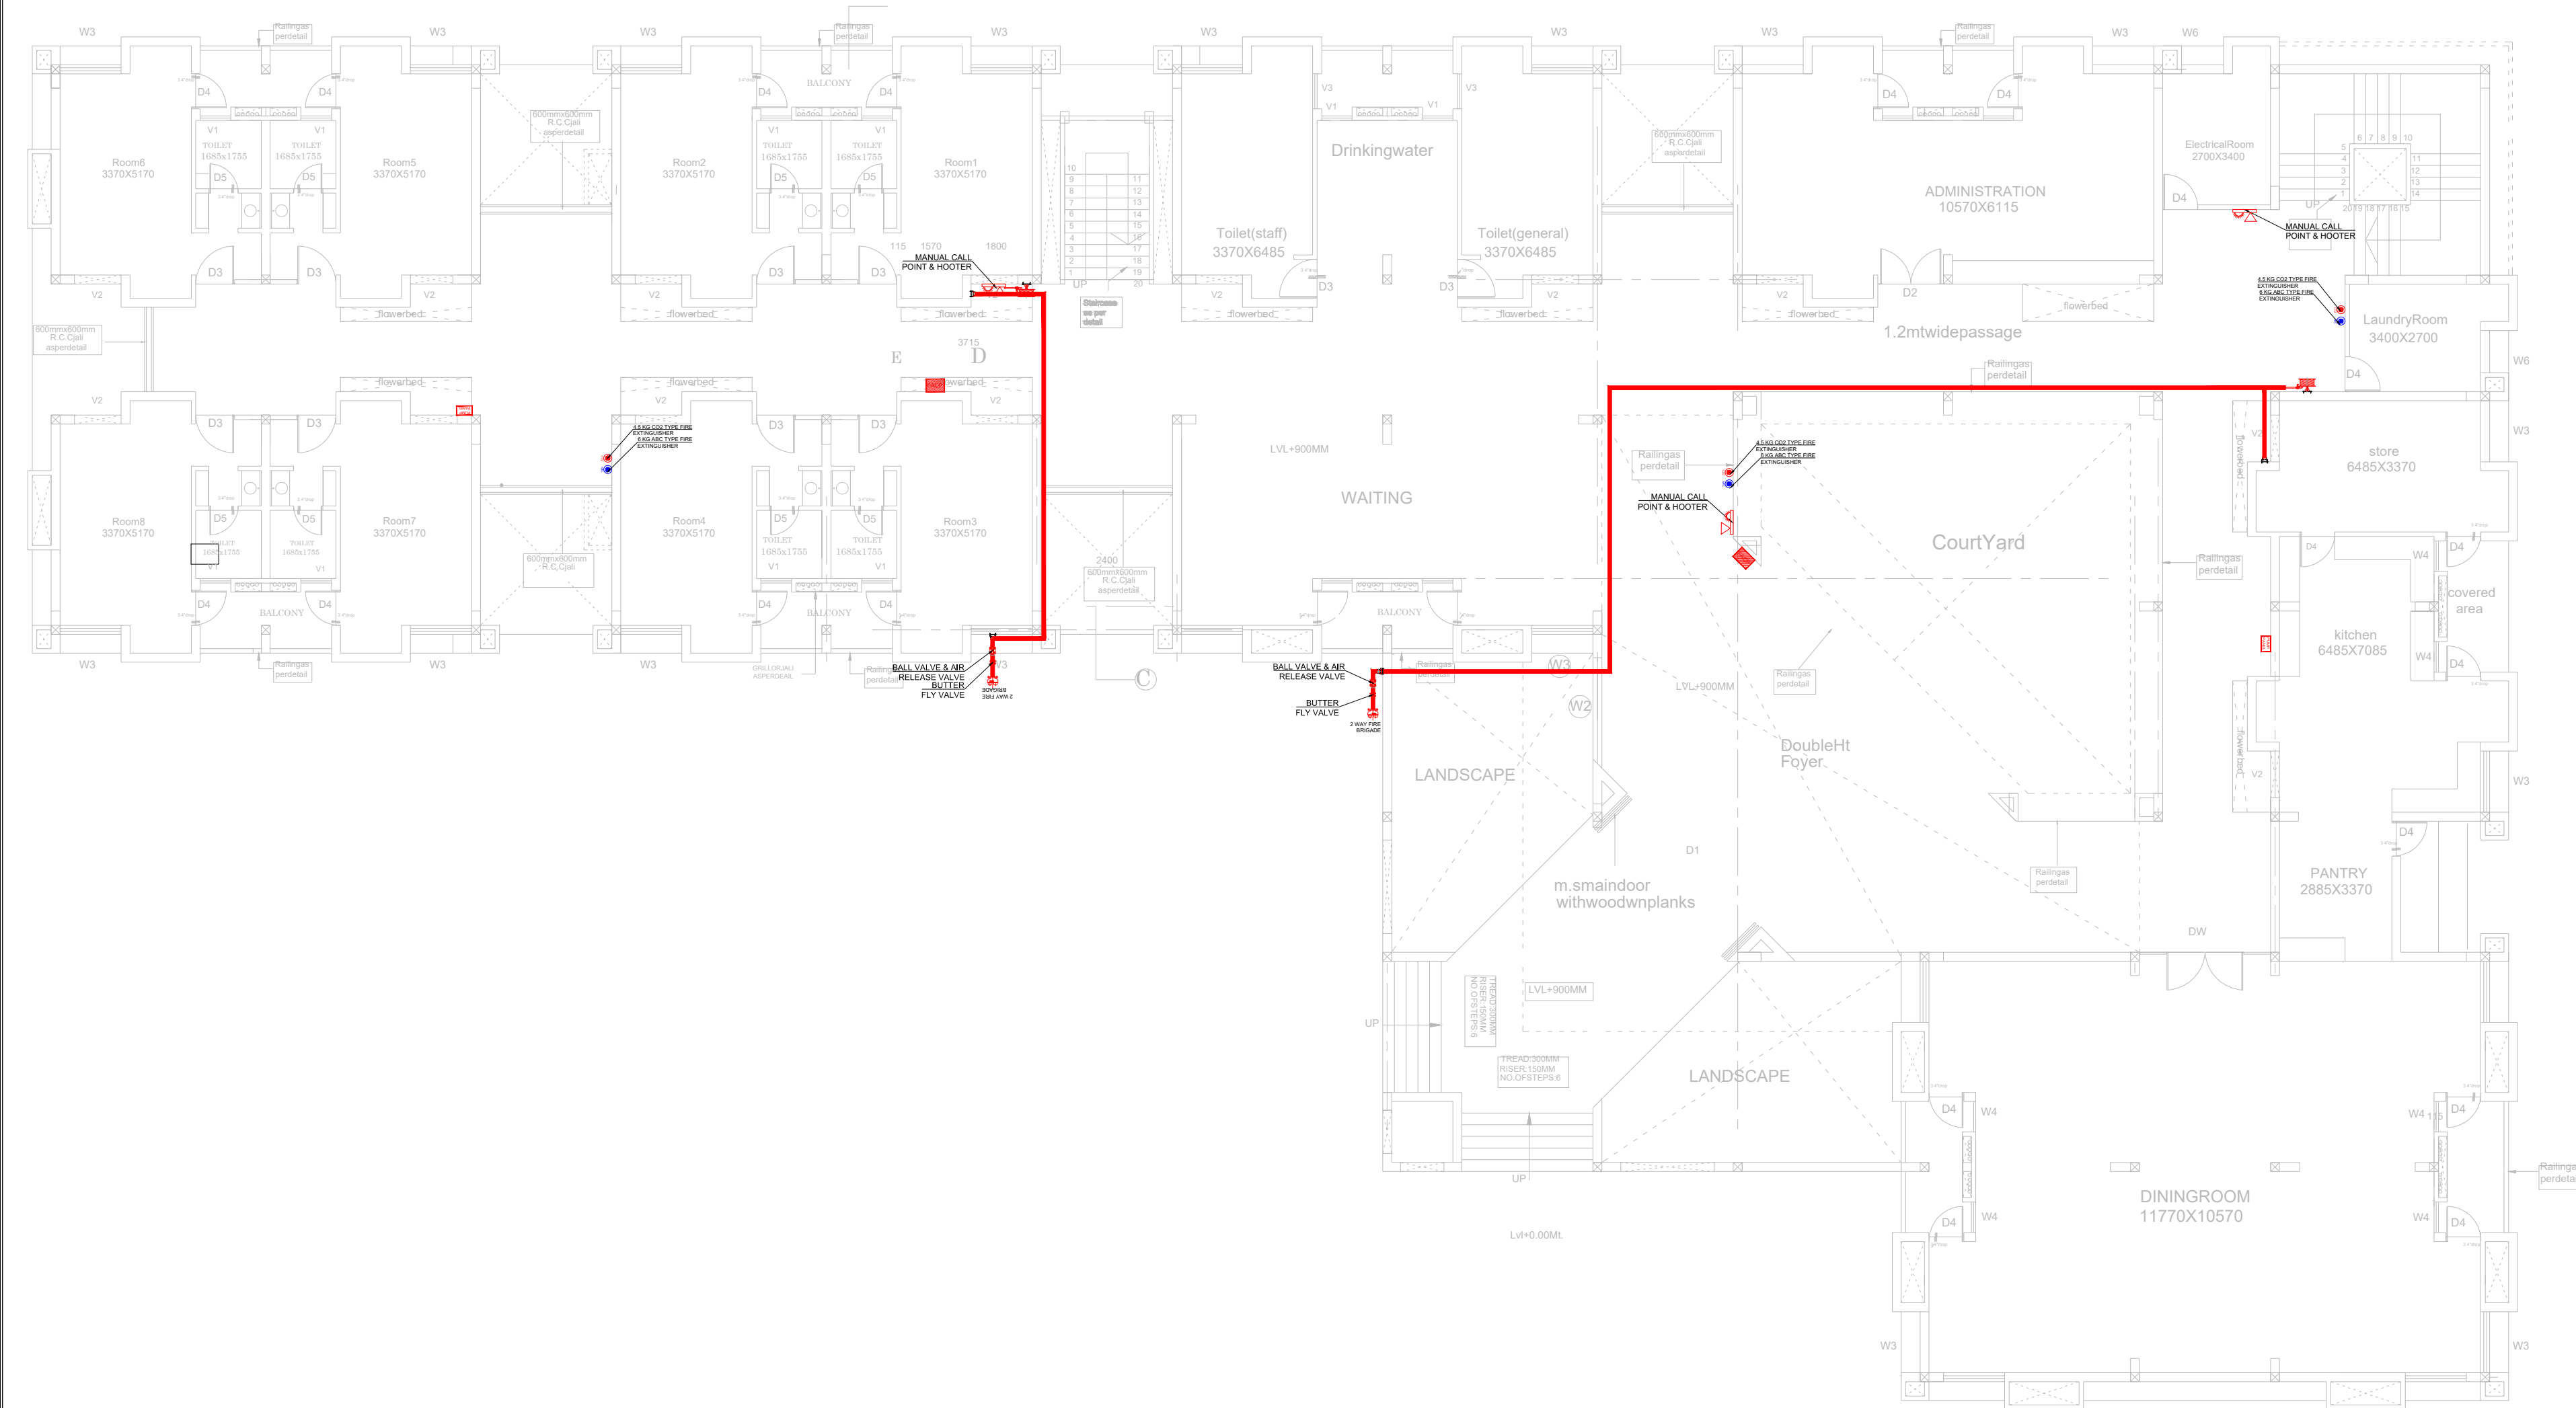

GROUND FLOOR

CLIENT:-

GSFC LTD BARODA

PROJECT ARCHITECT:-

VIJAY MATAI & ASSOCIATES

B-5 BOMBAY SHOPPING CENTRE R. C. DUTT ROAD, ALKAPURI ,
VADODARA-390005. Ph : (0265) 2344785

CONSULTANT:

REGD. OFFICE
52, MANGALJYOT SOCIETY NR. JYOTI PARK
SOCIETY KARELIBAUG VADODARA-18
HEAD OFFICE
219-C, 2ND FLOOR LOTUS AURA 2, BESIDES
IOCL PETROL PUMP, SAMA SAVLI ROAD,
VADODARA
CONTACT: +91 9898024352
EMAIL: aquaintegratedsolutions@gmail.com

DRAWING TITLE:-
HOSTEL BLOCK
GROUND FLOOR
FIRE SAFETY SYSTEM LAYOUT

DRAWING NO:- AIS_GSFC_FF_11

SHEET NO:- SHEET-1 OF 5

NORTH:-




NOTES:

- DO NOT SCALE THE DRAWING.
- ALL DIMENSIONS ARE IN METER.
- ALL MEASUREMENTS ARE TO BE CHECKED AND VERIFIED ON THE SITE.
- ANY DISCREPANCIES IN DRAWINGS MUST BE CLARIFIED WITH THE CONSULTANT PRIOR TO EXECUTION.

LEGEND:-

	TERRACE BOOSTER PUMP 900 LPM
	100Ø FIRE DOWNCOMER
	BALL VALVE
	FIRST AID HOSE REEL WITH DRUM
	2WAY FIRE BRIGADE
	FA CABLE-2C X 1.5 SM
	HOOTER / MANUAL CALL POINT
	FIRE ALARM CONTROL PANEL
	BFV- BUTTERFLY VALVE
	G.I. PIPE
	FIRE PUMP PANEL
	Co2 TYPE FIRE EXTINGUISHER (4.5 KG.)
	ABC TYPE FIRE EXTINGUISHER (6 KG.)

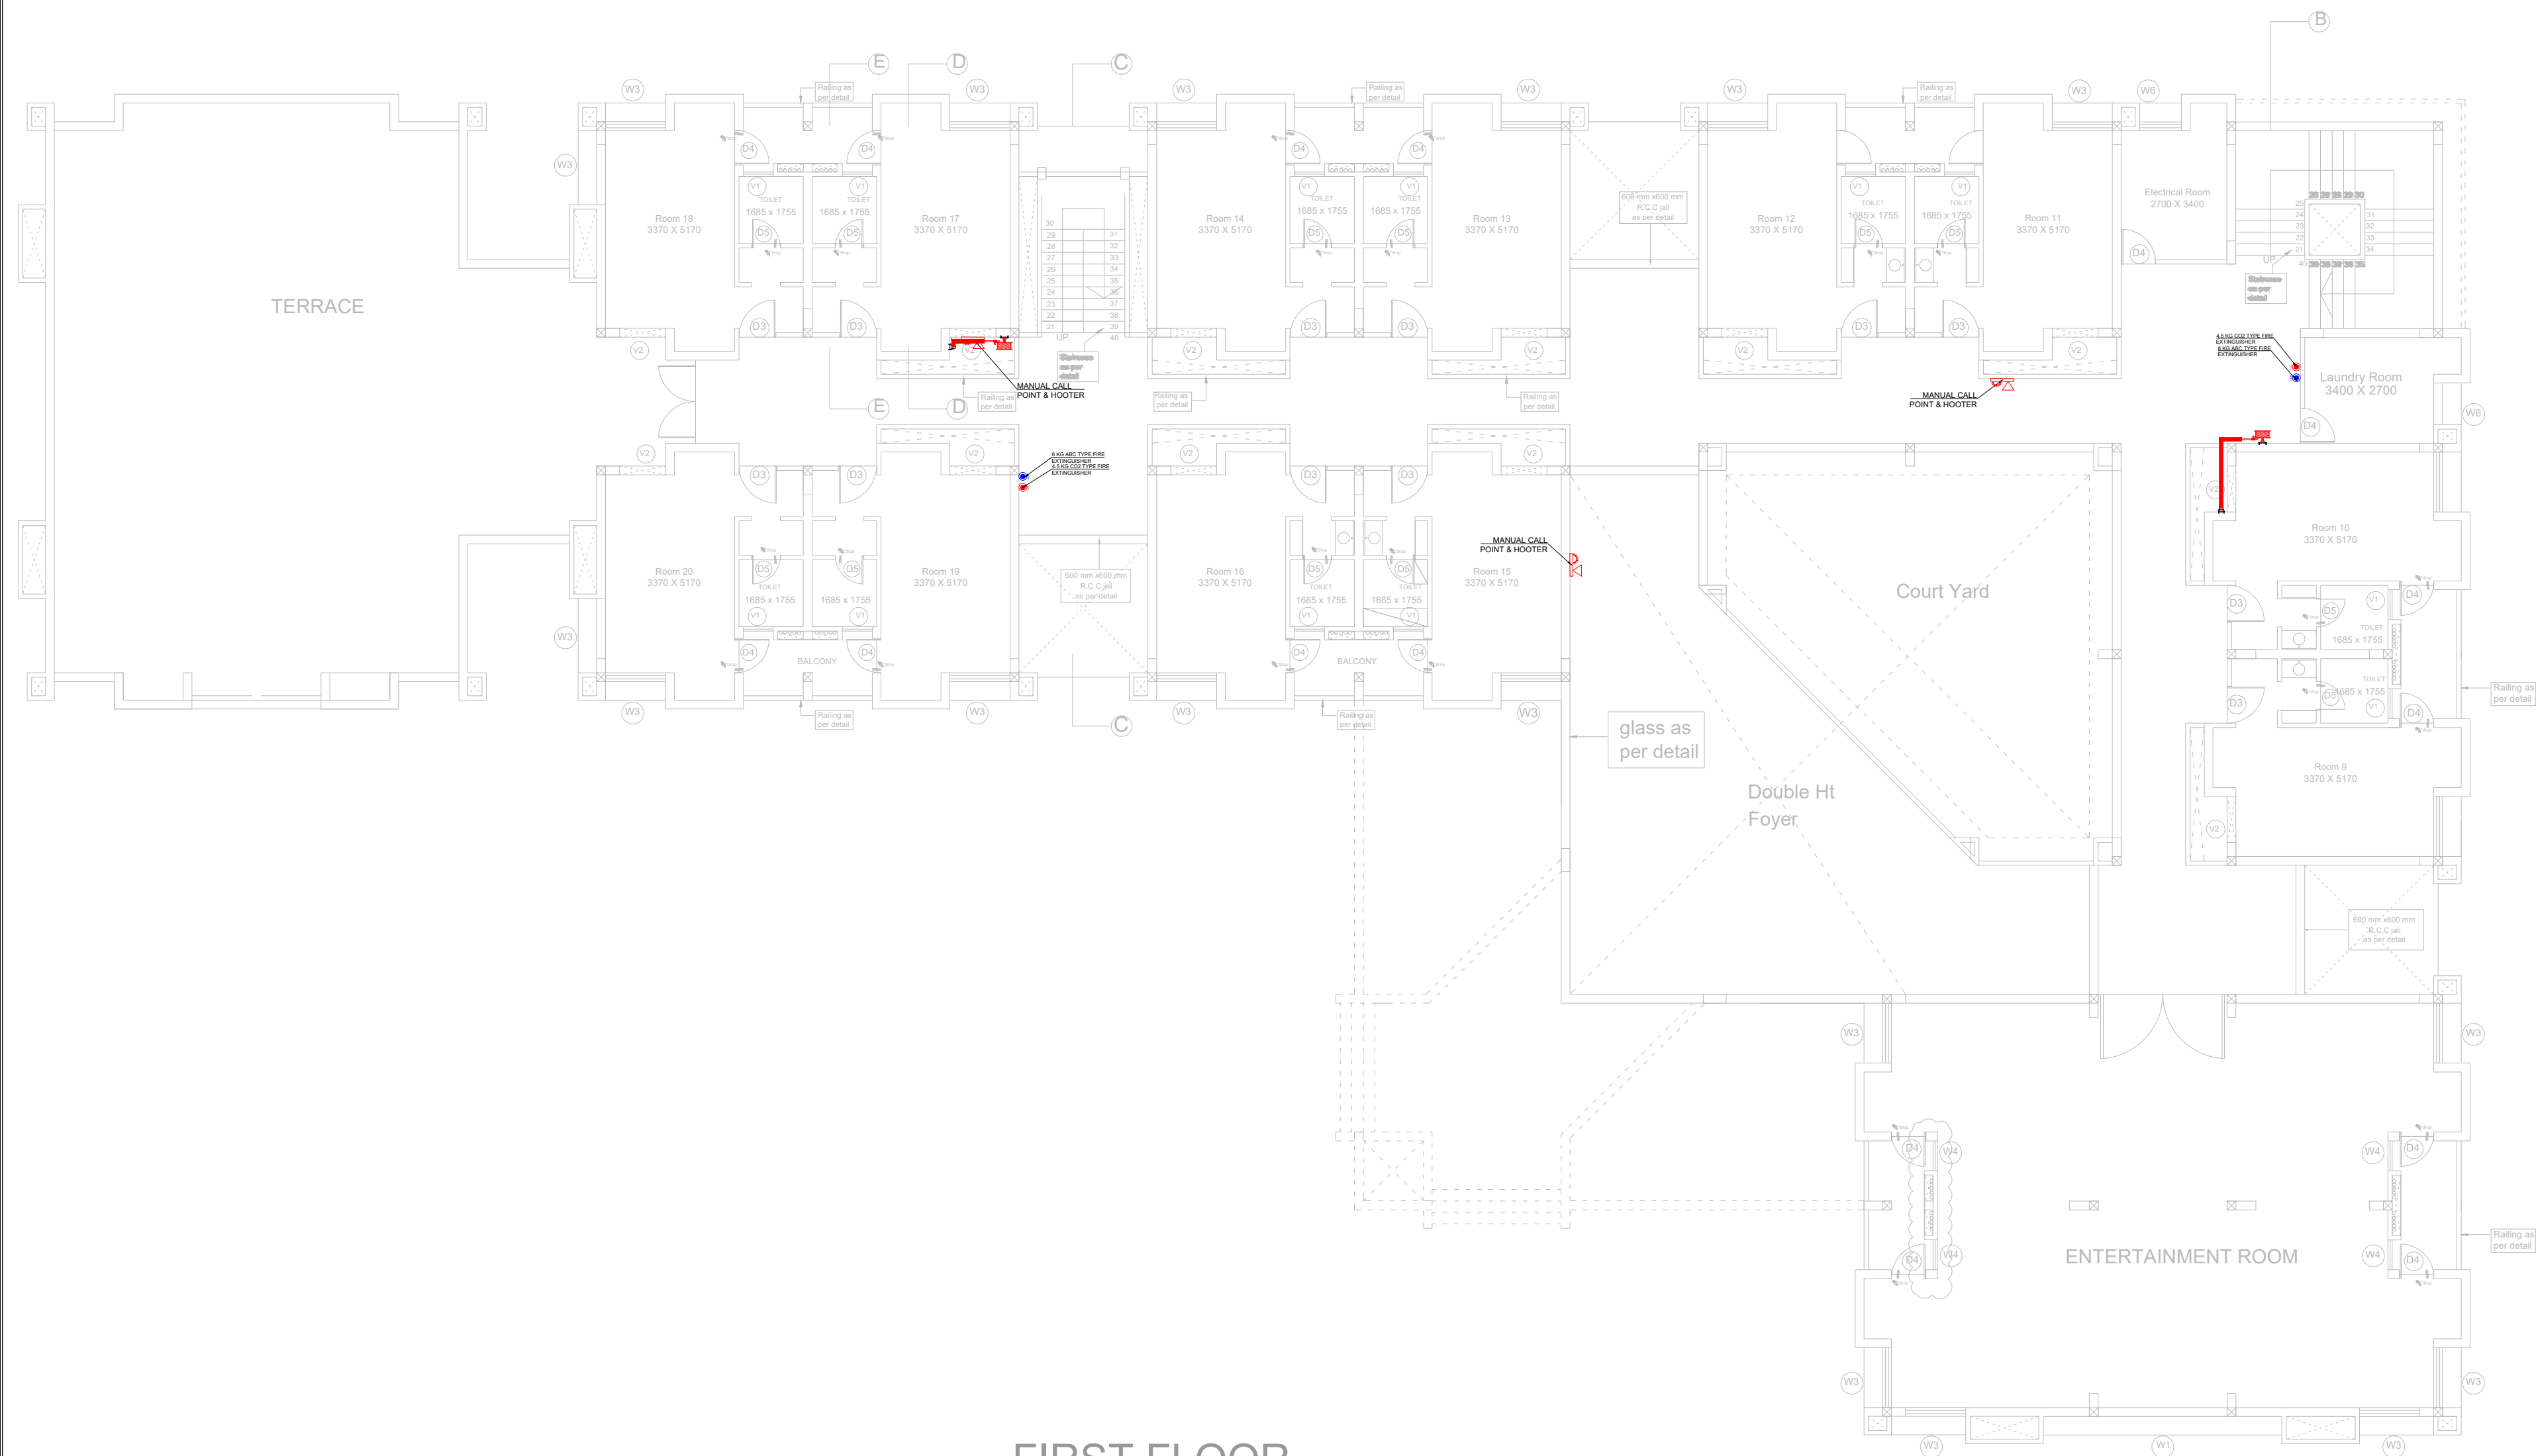

FIRST FLOOR

CLIENT:-

GSFC LTD BARODA

PROJECT ARCHITECT:-

VIJAY MATAI & ASSOCIATES

B-5 BOMBAY SHOPPING CENTRE R. C. DUTT ROAD, ALKAPURI ,
VADODARA-390005. Ph : (0265) 2344785

CONSULTANT:

**AQUA**
Integrated Solutions
(EPC & Consultancy Services)

REGD. OFFICE
52, MANGALJYOT SOCIETY NR. JYOTI PARK
SOCIETY KARELIBAUG VADODARA-18
HEAD OFFICE
219-C, 2ND FLOOR LOTUS AURA 2, BESIDES
KOCL PETROL PUMP, SAMA SAVLI ROAD,
VADODARA
CONTACT: +91 9898024352
EMAIL: aquaintegratedsolutions@gmail.com

DRAWING TITLE:- HOSTEL BLOCK
FIRST FLOOR
FIRE SAFETY SYSTEM LAYOUT

DRAWING NO:- AIS_GSFC_FF_12

SHEET NO:- SHEET-2 OF 5

NORTH:-



NOTES:

- DO NOT SCALE THE DRAWING.
- ALL DIMENSIONS ARE IN METER.
- ALL MEASUREMENTS ARE TO BE CHECKED AND VERIFIED ON THE SITE.
- ANY DISCREPANCIES IN DRAWINGS MUST BE CLARIFIED WITH THE CONSULTANT PRIOR TO EXECUTION.

LEGEND:-

	TERRACE BOOSTER PUMP 900 LPM
	100Ø FIRE DOWNCOMER
	BALL VALVE
	FIRST AID HOSE REEL WITH DRUM
	2WAY FIRE BRIGADE
	FA CABLE-2C X 1.5 SM
	HOOTER / MANUAL CALL POINT
	FIRE ALARM CONTROL PANEL
	BFV- BUTTERFLY VALVE
	G.I. PIPE
	FIRE PUMP PANEL
	Co2 TYPE FIRE EXTINGUISHER (4.5 KG.)
	ABC TYPE FIRE EXTINGUISHER (6 KG.)

CLIENT:-

GSFC LTD BARODA

PROJECT ARCHITECT:-

VIJAY MATAI & ASSOCIATES

B-5 BOMBAY SHOPPING CENTRE R. C. DUTT ROAD, ALKAPURI ,
VADODARA-390005. Ph : (0265) 2344785

CONSULTANT:

REGD. OFFICE
52, MANGALJYOT SOCIETY NR. JYOTI PARK
SOCIETY KARELIBAUG VADODARA-18
HEAD OFFICE
219-C, 2ND FLOOR LOTUS AURA 2, BESIDES
IOCL PETROL PUMP, SAMA SAVLI ROAD,
VADODARA
CONTACT: +91 9898024352
EMAIL: aequintegratedsolutions@gmail.com

DRAWING TITLE:- HOSTEL BLOCK
SECOND FLOOR
FIRE SAFETY SYSTEM LAYOUT


DRAWING NO:- AIS_GSFC_FF_13


SHEET NO:- SHEET-3 OF 5

NORTH:-



SECOND FLOOR

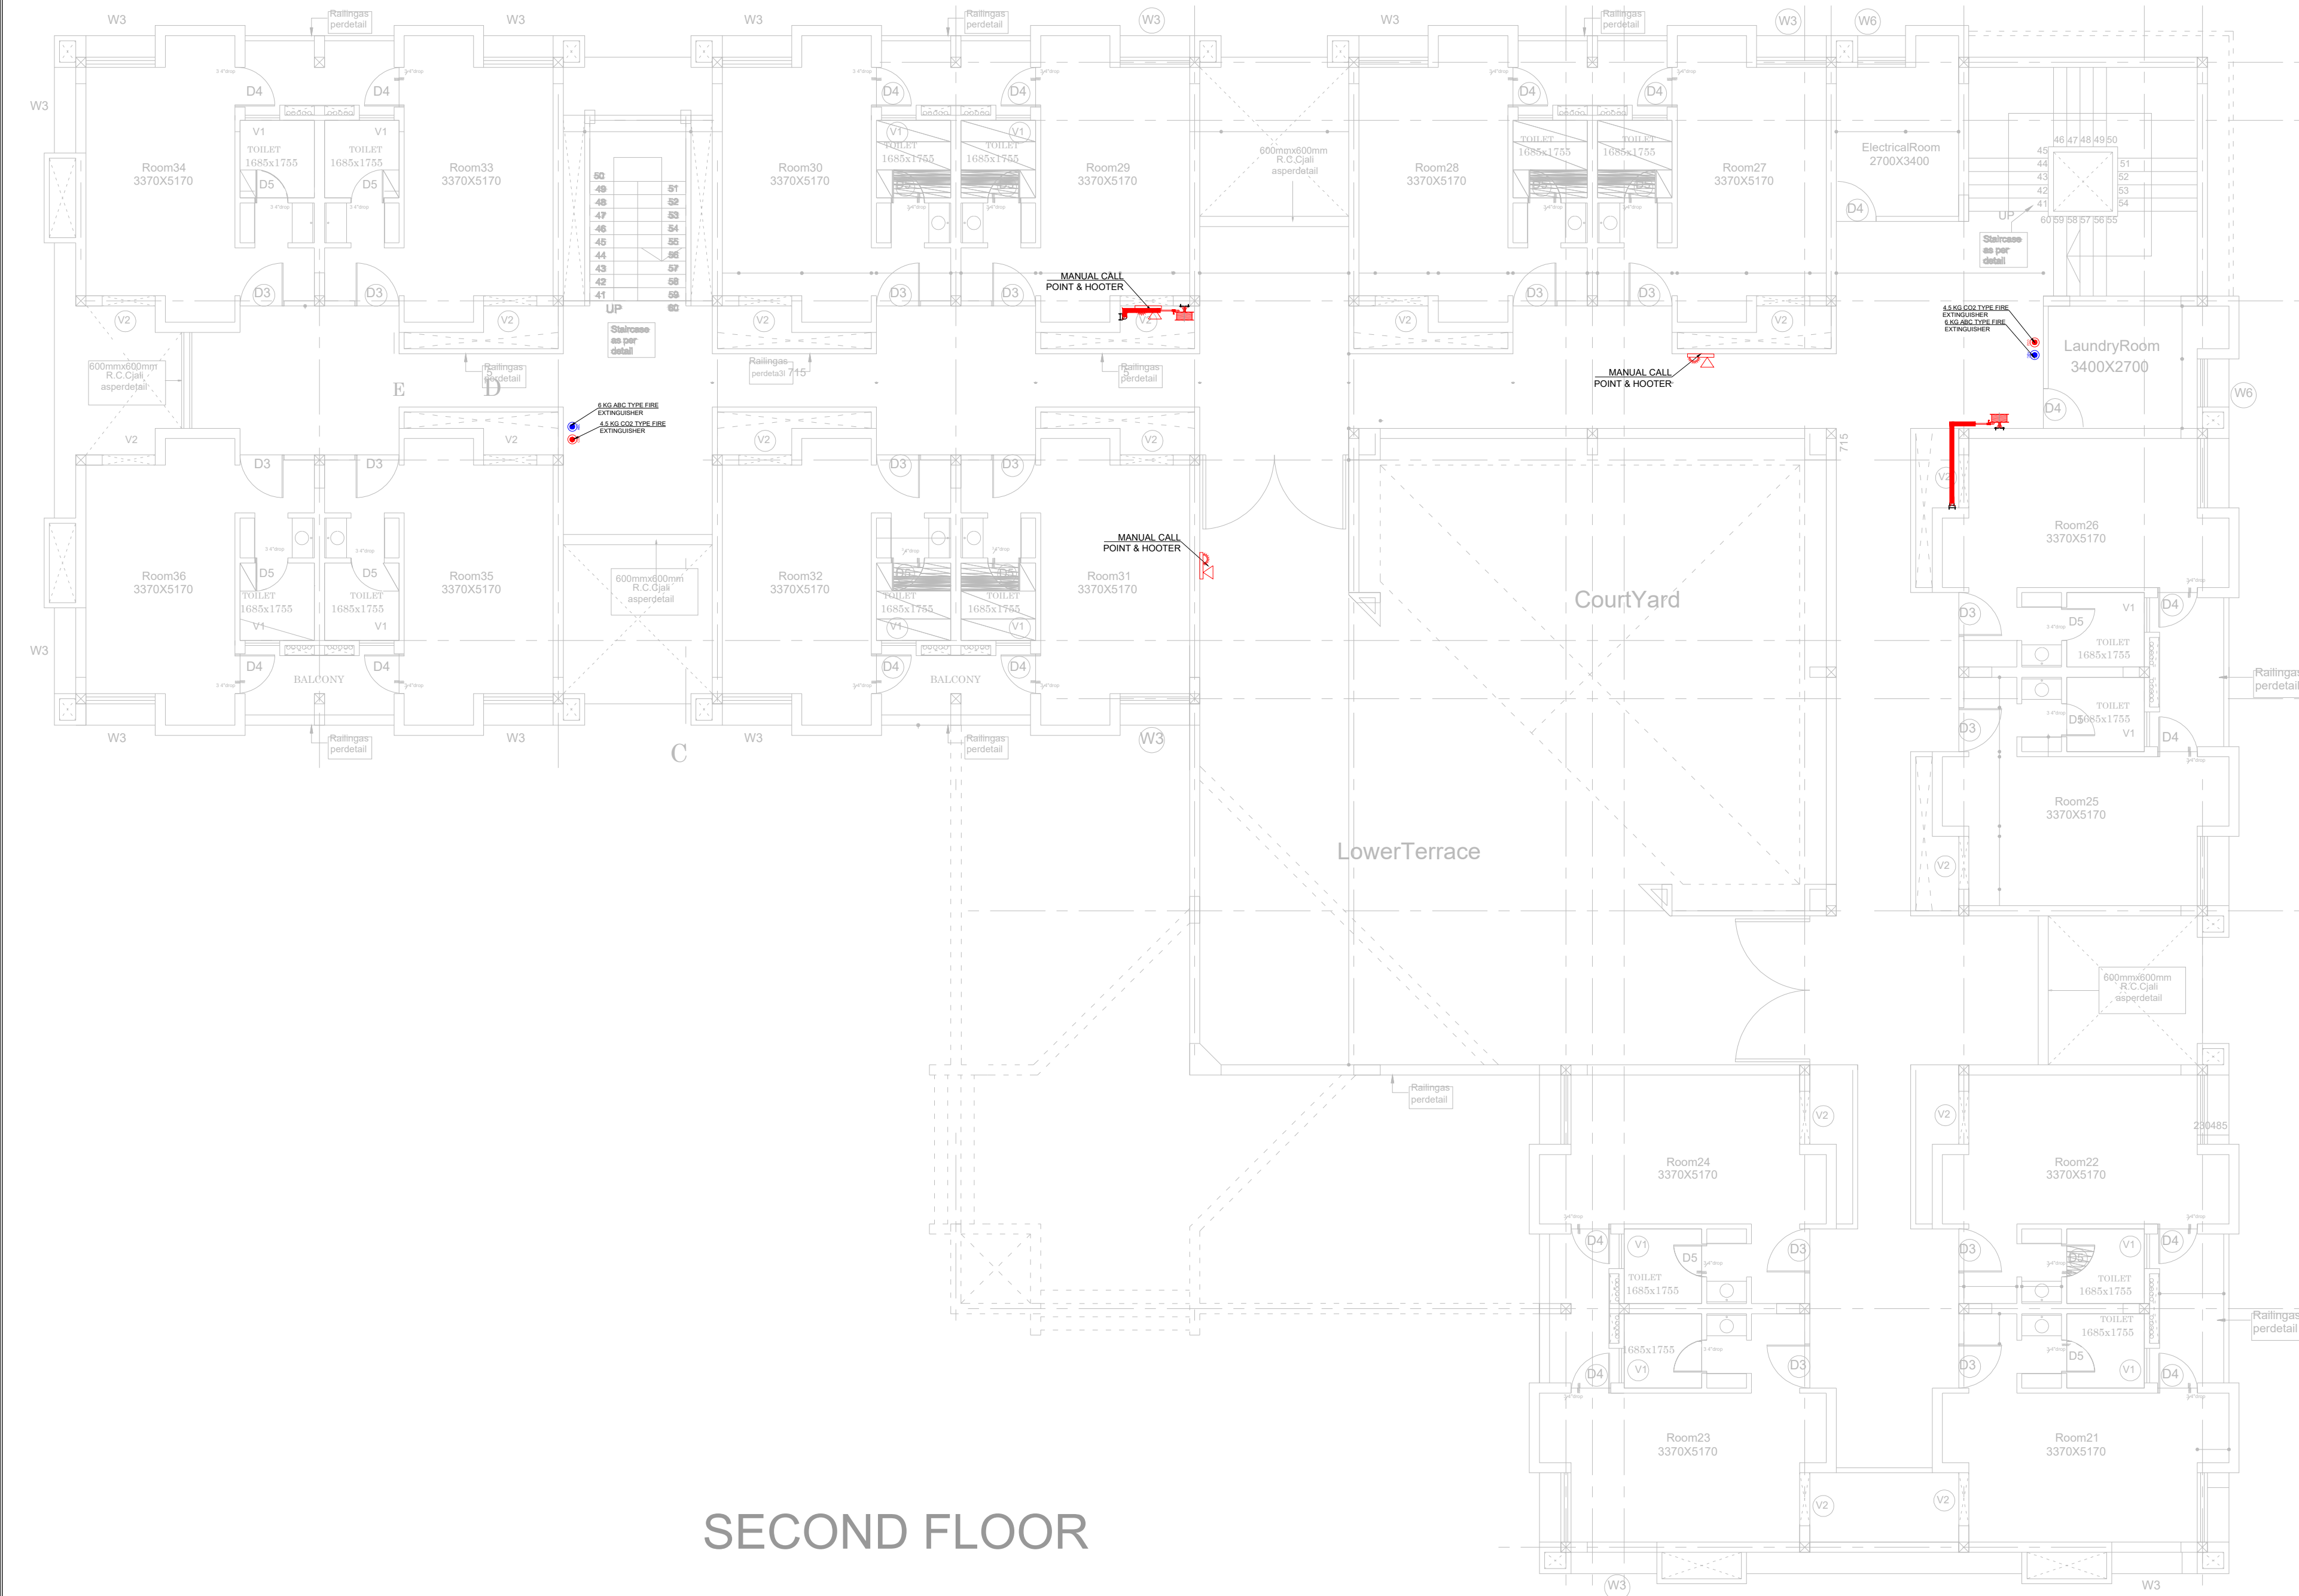

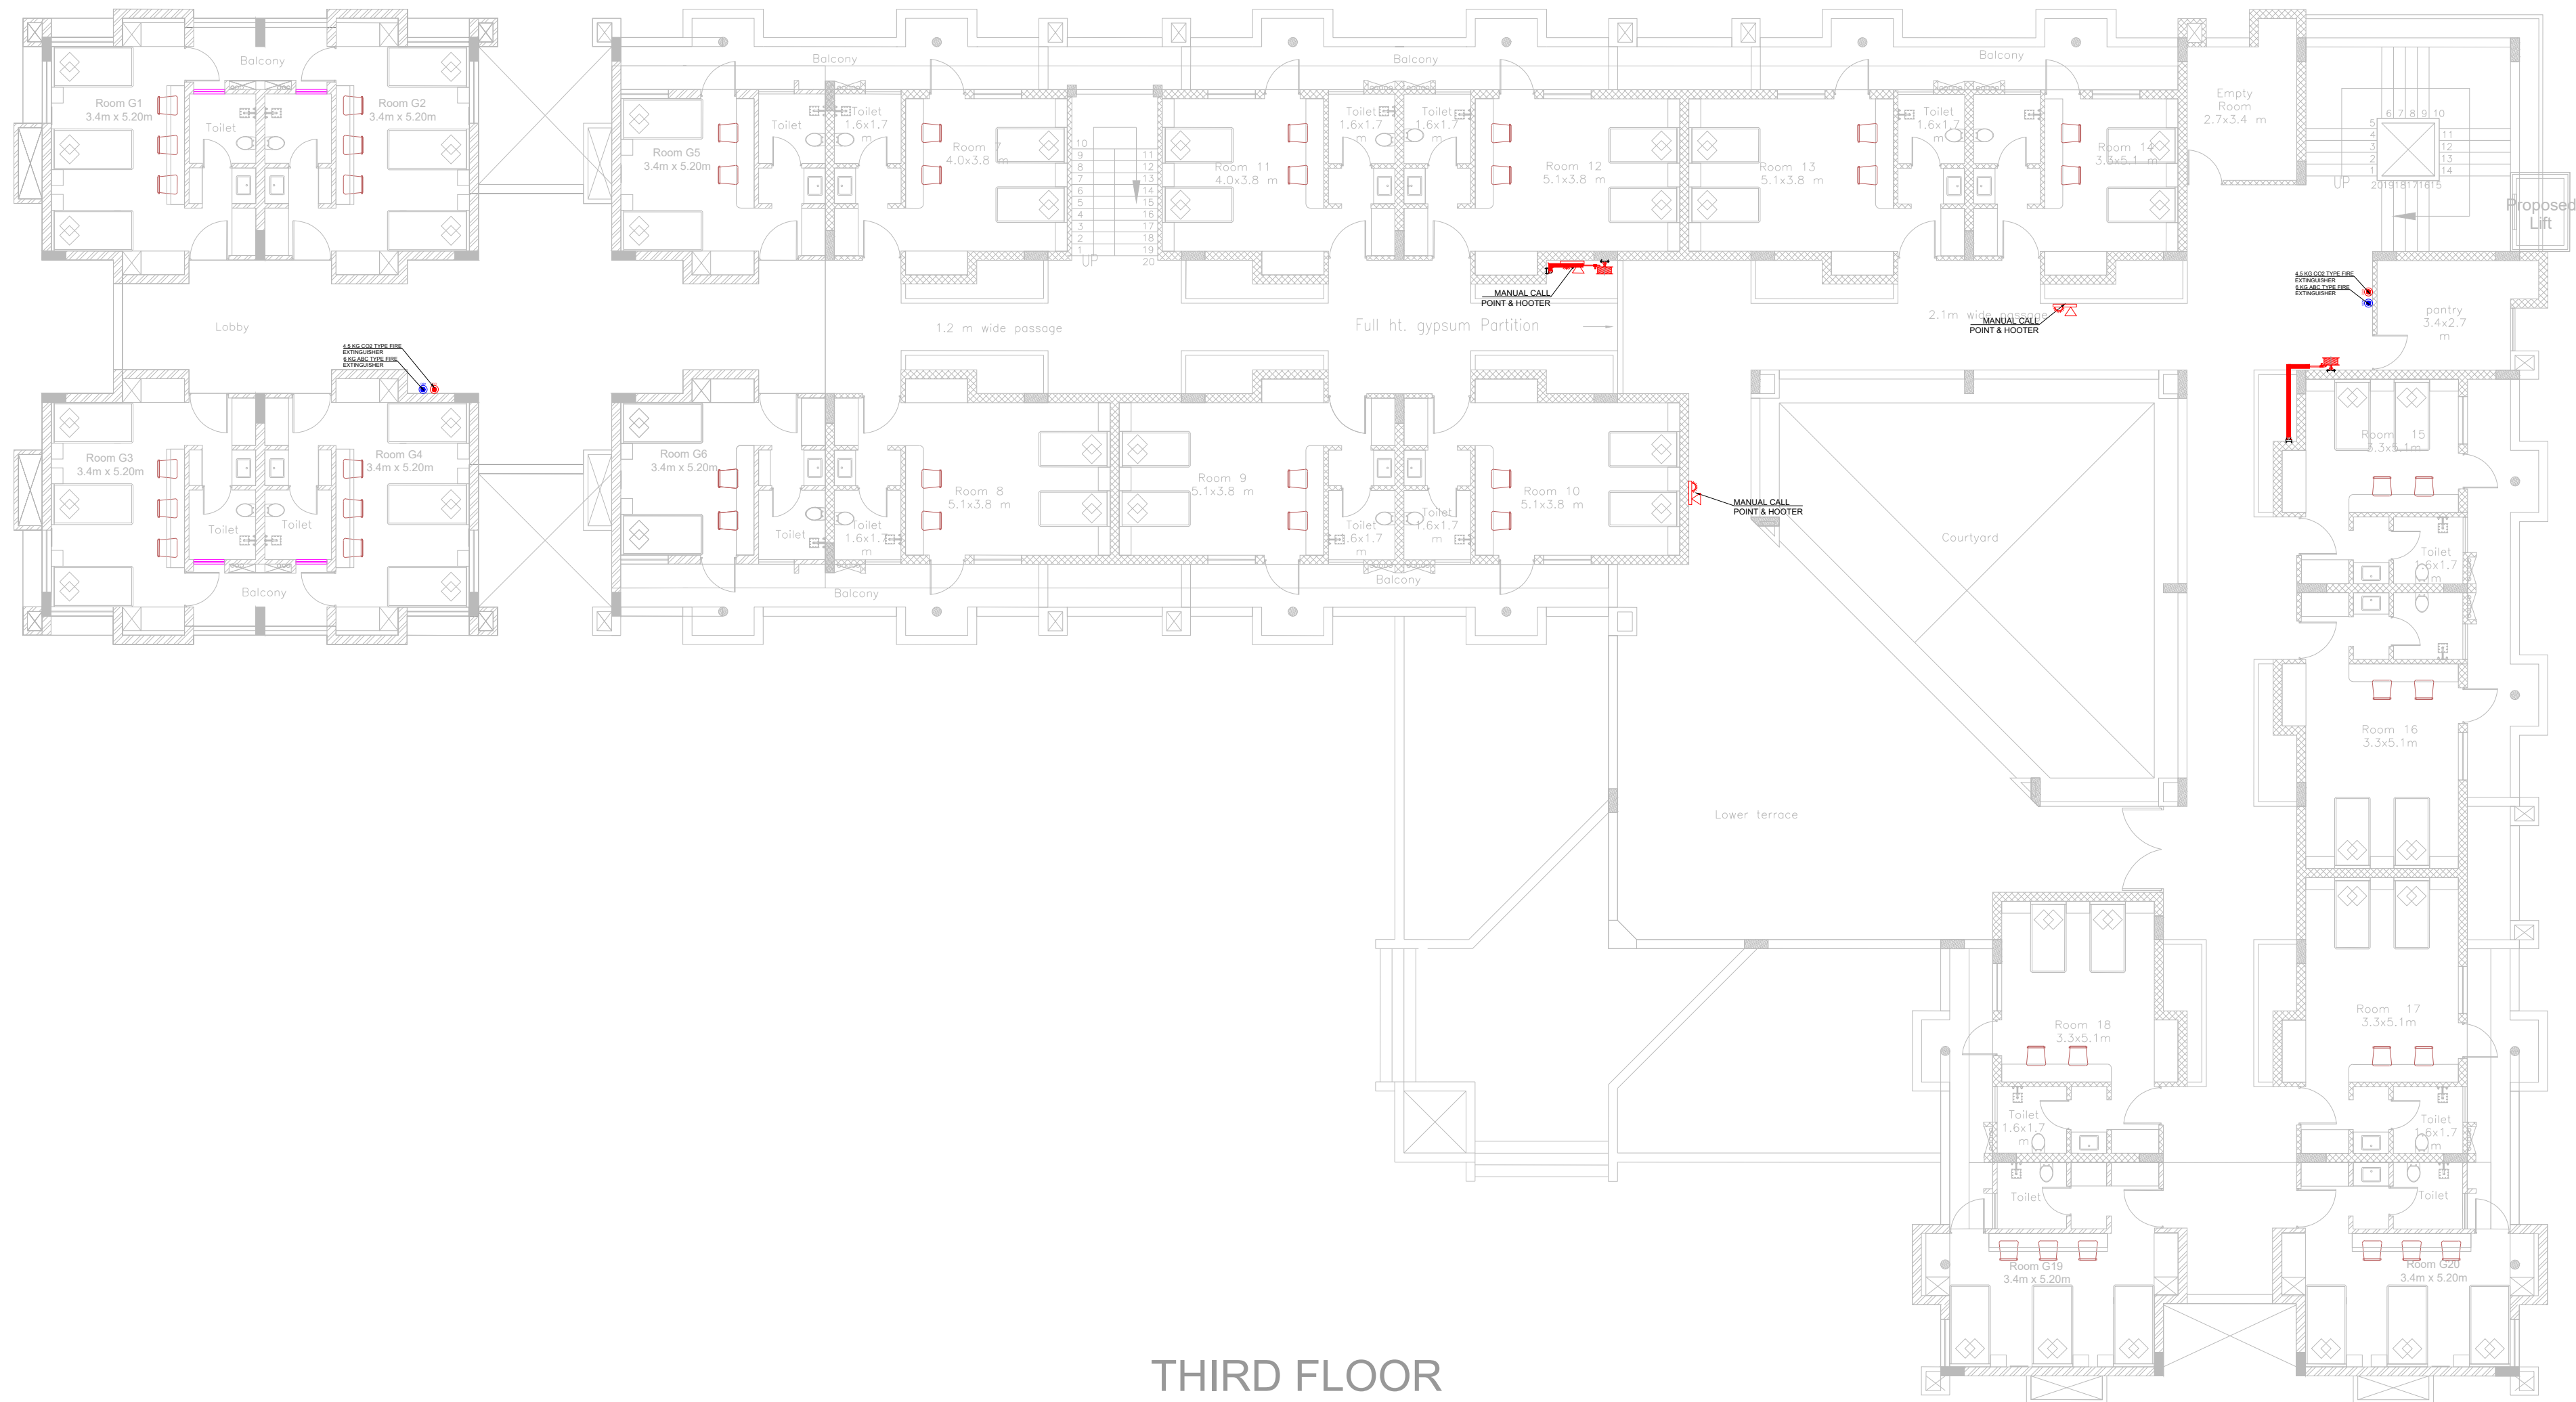

NOTES:

1. DO NOT SCALE THE DRAWING.
2. ALL DIMENSIONS ARE IN METER.
3. ALL MEASUREMENTS ARE TO BE CHECKED AND VERIFIED ON THE SITE.
4. ANY DISCREPANCIES IN DRAWINGS MUST BE CLARIFIED WITH THE CONSULTANT PRIOR TO EXECUTION.

LEGEND:-

	TERRACE BOOSTER PUMP 900 LPM
	100Ø FIRE DOWNCOMER
	BALL VALVE
	FIRST AID HOSE REEL WITH DRUM
	2WAY FIRE BRIGADE
	FA CABLE-2C X 1.5 SM
	HOOTER / MANUAL CALL POINT
	FIRE ALARM CONTROL PANEL
	BFV- BUTTERFLY VALVE
	G.I. PIPE
	FIRE PUMP PANEL
	Co2 TYPE FIRE EXTINGUISHER (4.5 KG.)
	ABC TYPE FIRE EXTINGUISHER (6 KG.)

CLIENT:-

GSFC LTD BARODA

PROJECT ARCHITECT:-

VIJAY MATAI & ASSOCIATES

B-5 BOMBAY SHOPPING CENTRE R. C. DUTT ROAD, ALKAPURI ,
VADODARA-390005. Ph : (0265) 2344785

CONSULTANT:

 **AQUA**
Integrated Solutions
(EPC & Consultancy Services)

REGD. OFFICE
52, MANGALJYOT SOCIETY NR. JYOTI PARK
SOCIETY KARELIBAUG VADODARA-18
HEAD OFFICE
219-C, 2ND FLOOR LOTUS AURA 2, BESIDES
IOCL PETROL PUMP, SAMA SAVLI ROAD,
VADODARA
CONTACT: +91 9898024352
EMAIL: aquaintegratedsolutions@gmail.com

DRAWING TITLE:-

HOSTEL BLOCK
THIRD FLOOR
FIRE SAFETY SYSTEM LAYOUT

DRAWING NO:-

AIS_GSFC_FF_14

SHEET NO:-

SHEET-4 OF 5

NORTH:-



NOTES:
1. DO NOT SCALE THE DRAWING.
2. ALL DIMENSIONS ARE IN METER.
3. ALL MEASUREMENTS ARE TO BE CHECKED AND VERIFIED ON THE SITE.
4. ANY DISCREPANCIES IN DRAWINGS MUST BE CLARIFIED WITH THE CONSULTANT PRIOR TO EXECUTION.

LEGEND:-	
	TERRACE BOOSTER PUMP 900 LPM
	100Ø FIRE DOWNCOMER
	BALL VALVE
	FIRST AID HOSE REEL WITH DRUM
	2WAY FIRE BRIGADE
	FA CABLE-2C X 1.5 SM
	HOOTER / MANUAL CALL POINT
	FIRE ALARM CONTROL PANEL
	BFV- BUTTERFLY VALVE
	G.I. PIPE
	FIRE PUMP PANEL
	Co2 TYPE FIRE EXTINGUISHER (4.5 KG.)
	ABC TYPE FIRE EXTINGUISHER (6 KG.)

CLIENT:-
GSFC LTD BARODA


PROJECT ARCHITECT:-
VIJAY MATAI & ASSOCIATES
B-5 BOMBAY SHOPPING CENTRE R. C. DUTT ROAD, ALKAPURI ,
VADODARA-390005. Ph : (0265) 2344785

CONSULTANT:

REGD. OFFICE
52, MANGALJYOT SOCIETY NR. JYOTI PARK
SOCIETY KARELIBAUG VADODARA-18
HEAD OFFICE
219-C, 2ND FLOOR LOTUS AURA 2, BESIDES
IOCL PETROL PUMP, SAMA SAVLI ROAD,
VADODARA
CONTACT: +91 9898024352
EMAIL: aquaintegratedsolutions@gmail.com

DRAWING TITLE:-
HOSTEL BLOCK
TERRACE FLOOR
FIRE SAFETY SYSTEM LAYOUT

DRAWING NO:- AIS_GSFC_FF_15	NORTH:-
SHEET NO:- SHEET-5 OF 5	

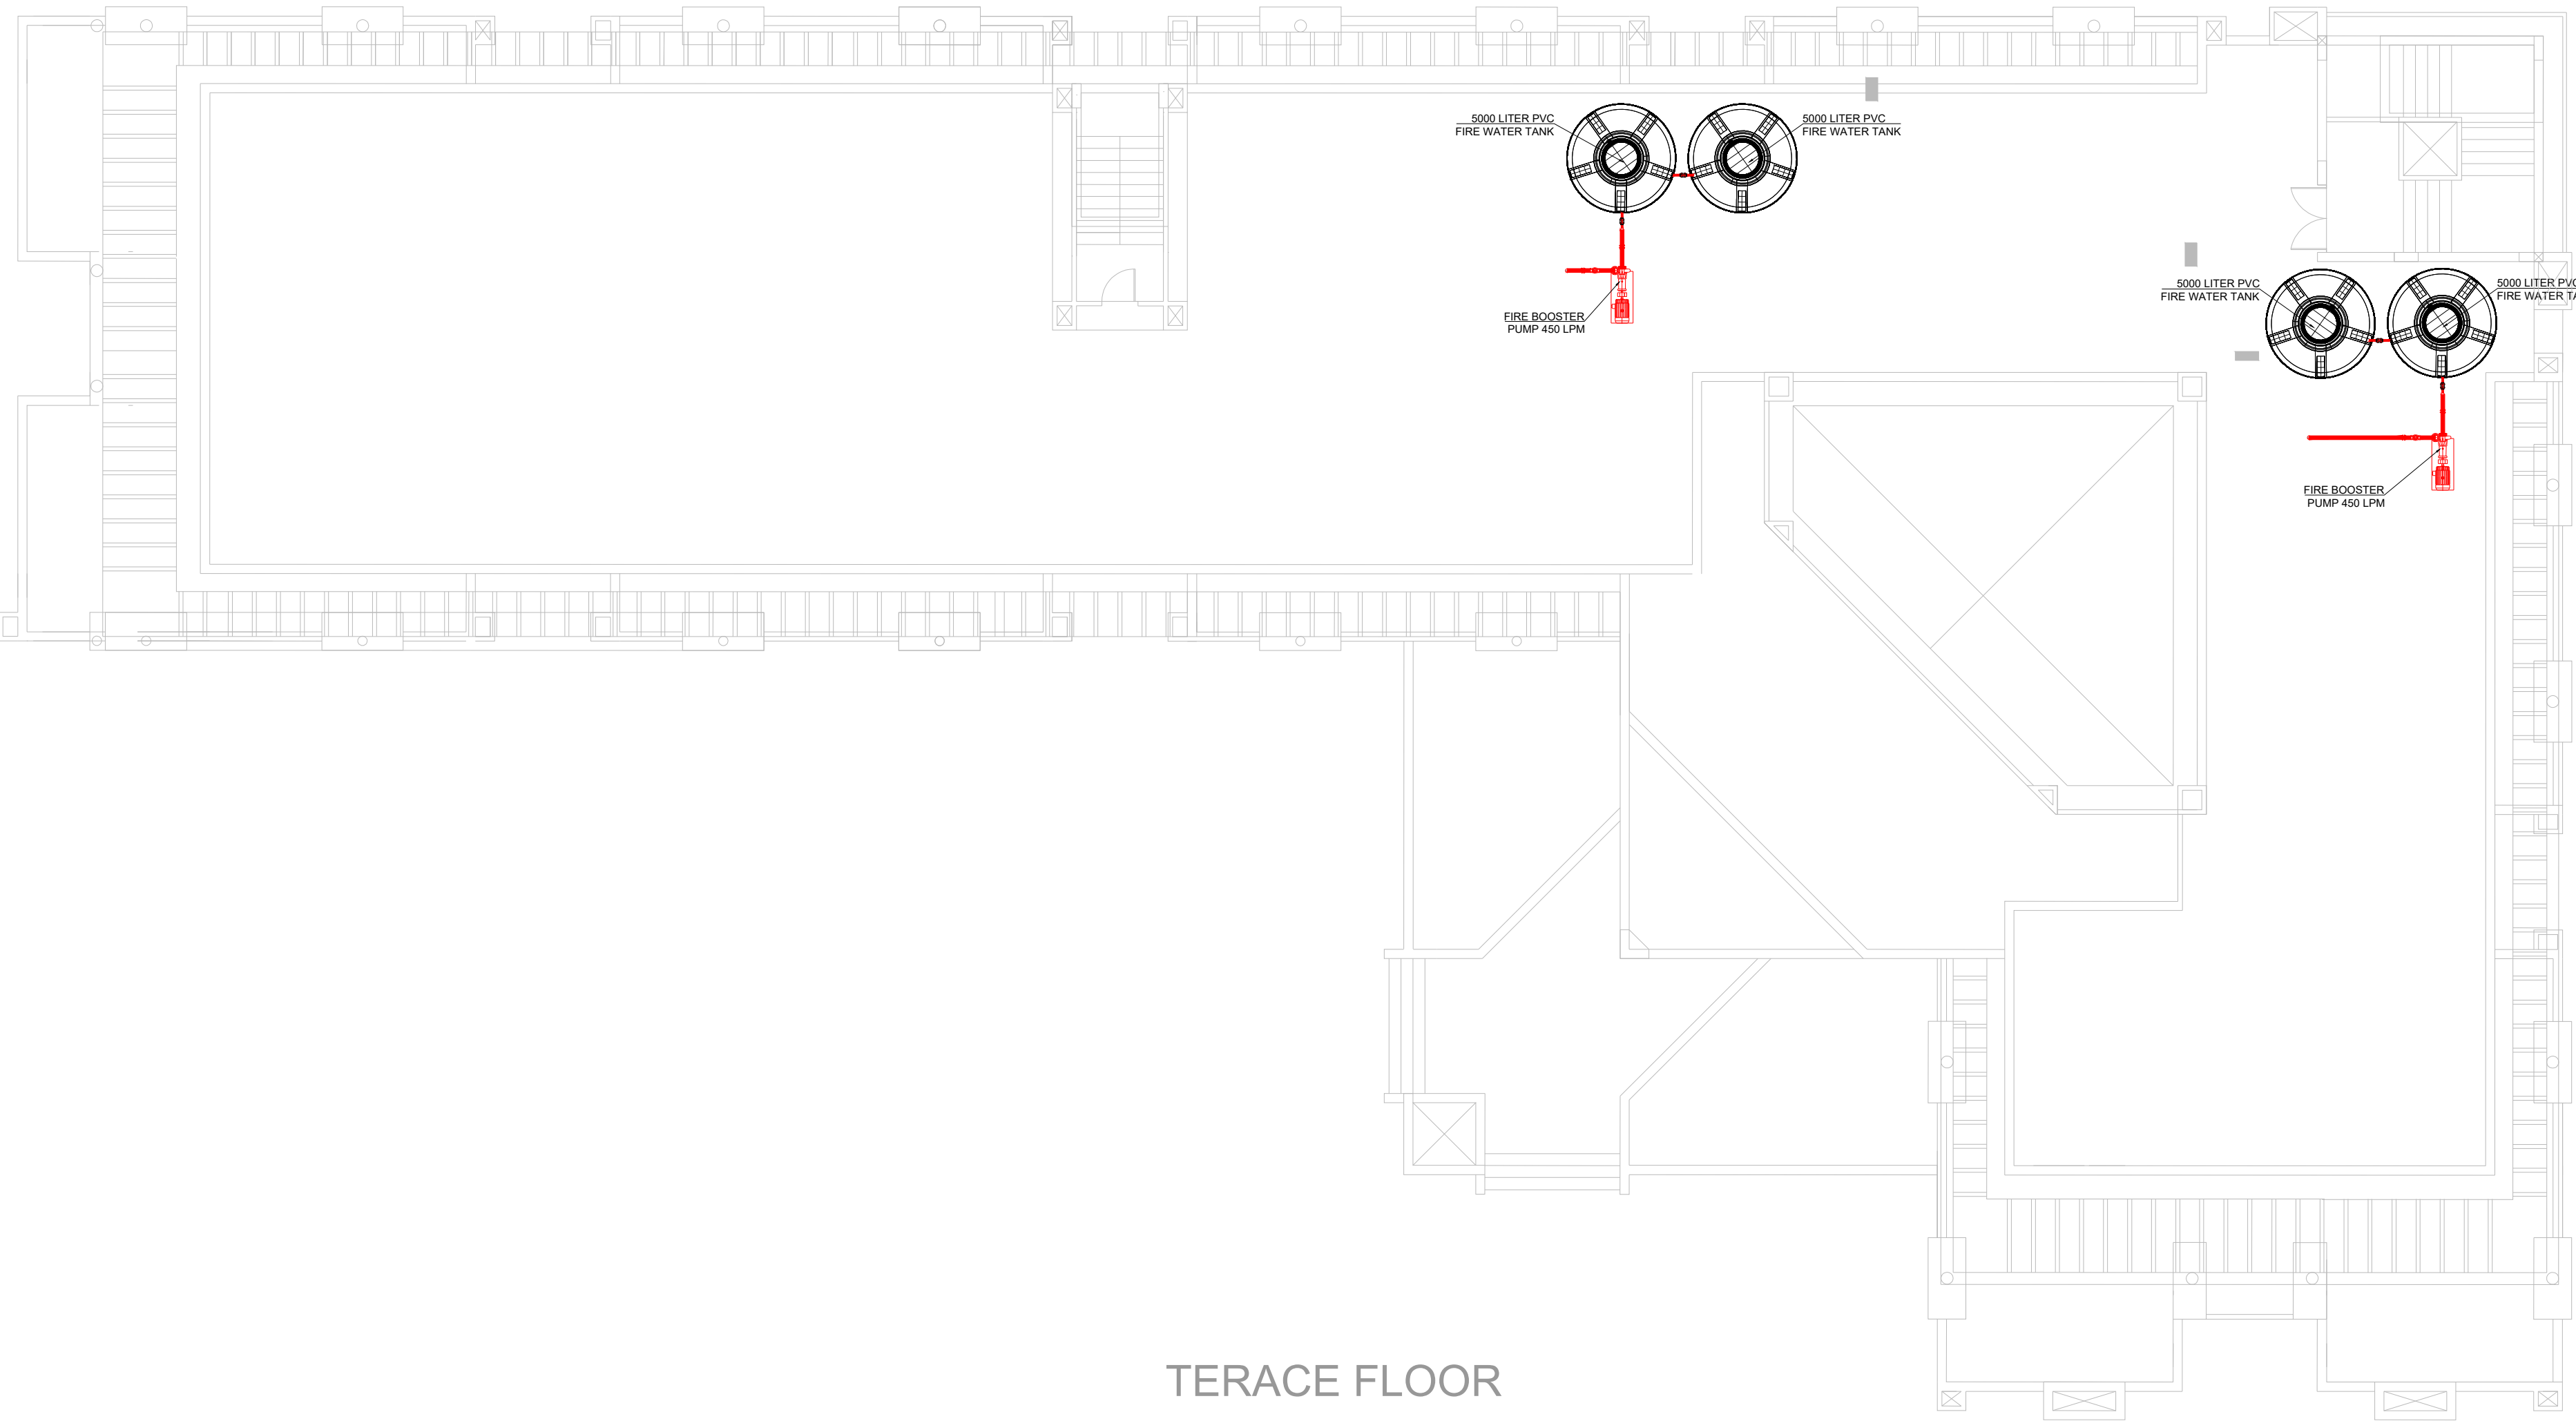

TERACE FLOOR